

Projet

Maître d'ouvrage : Nicolas RABOT

Adresse du projet : 455 chemin de Lasprades — 31250 Vaudreuille

Références cadastrales : section ZI — parcelle n°18

Objet de la demande : implantation de 6 habitations légères de loisirs démontables à usage touristique saisonnier, en zone Ntc.

La présente déclaration préalable constitue une nouvelle présentation du projet, établie à la suite du retour d'instruction relatif au précédent dossier de déclaration préalable n° DP 031 569 26 0 0001, déposé le 10/03/2026 pour la parcelle ZI n°18, située 455 chemin de Lasprades à Vaudreuille.

La demande ne porte pas sur la création d'un terrain de camping avec emplacements nus pour tentes, caravanes ou camping-cars. Elle concerne un projet limité à 6 HLL démontables à usage touristique saisonnier.

Le projet a été repris afin de répondre aux observations formulées par les services instructeurs, notamment concernant les accès, le stationnement, la gestion des déchets, l'alimentation en eau potable, le raccordement électrique et la gestion des eaux usées.

Le présent dossier concerne uniquement l'implantation de six habitations légères de loisirs démontables à usage touristique saisonnier, réparties comme suit :

- deux tipis démontables sur plancher bois ;
- deux yourtes démontables sur plancher bois ;
- deux cabanes démontables à ossature bois.

Les constructions projetées sont légères, démontables et réversibles. Elles sont posées sur planchers bois et appuis ponctuels réversibles, sans fondations maçonnées, sans scellement béton et sans terrassement lourd.

Le projet prévoit également des aménagements légers strictement nécessaires au fonctionnement des HLL :

- une zone de stationnement légère et perméable, localisée en partie basse du terrain, sans création de voirie lourde ni imperméabilisation significative ;
- un cheminement piéton permettant de rejoindre les HLL depuis la zone d'accès et de stationnement ;
- un local technique / sanitaire démontable, regroupant les usages communs du site ;
- un point de collecte des déchets intégré au fonctionnement du local ou localisé à proximité de l'accès selon les modalités de collecte retenues ;
- un raccordement projeté au réseau public d'eau potable ;
- un raccordement électrique général projeté ;
- un dispositif d'assainissement autonome compact de type filtre coco ou équivalent, dimensionné à titre indicatif sur une base minimale de 5 EH et soumis à validation du SPANC.

Les HLL ne sont pas raccordées individuellement aux réseaux. Les usages liés à l'eau, à l'électricité, à la recharge ponctuelle, aux sanitaires et à la gestion des eaux grises sont centralisés au niveau du local technique / sanitaire. Le local technique / sanitaire est conçu comme une structure légère démontable, sans fondation maçonnée, avec bardage bois naturel, couverture légère de type bac acier teinte gris anthracite et menuiseries bois. Il permet de regrouper les fonctions nécessaires à l'exploitation saisonnière du site : éviers, toilettes sèches, bacs de collecte, casiers de rangement et points de recharge.

Les surfaces des HLL ont été précisées et harmonisées dans l'ensemble du dossier :

- deux tipis de 23,76 m² chacun ;
- deux yourtes de 23,76 m² chacune ;
- deux cabanes de 20,00 m² chacune ;
- soit une surface totale créée de 135,04 m² pour les HLL.

Le plan de masse précise l'implantation des six HLL, les arbres concernés par le projet, les accès existants, les cheminements légers, les limites de la zone Ntc, le stationnement léger, le local technique / sanitaire, les points de raccordement projetés et le principe d'assainissement autonome compact.

Les tracés de réseaux représentés au plan sont des tracés de principe, à confirmer avec les gestionnaires compétents.

L'implantation définitive du dispositif d'assainissement sera soumise à validation du SPANC.

Cette nouvelle demande vise donc à présenter un projet limité, réversible et adapté au caractère naturel et boisé du site, tout en intégrant les équipements strictement nécessaires à son fonctionnement et aux demandes formulées lors de l'instruction du dossier précédent.

Maitre d'ouvrage: NICOLAS RABOT 455 Chemin de Lasprades VAUDREUILLE FR	Ouvrage: Implantation de 6 HLL démontables Zone Ntc	Adresse du projet: 455 Chemin de Lasprades 31250 VAUDREUILLE	
Références: section ZI parcelle 18	Planche: NOTE D'ACCOMPAGNEME NT	Echelle :	
		N° de plan: DPC0	Date :06/07/2026



Carte IGN




500 m




300 m

Le projet se situe sur la parcelle ZI n°18, au sein d'un secteur classé en zone Ntc du document d'urbanisme.


Maitre d'ouvrage: NICOLAS RABOT 455 Chemin de Lasprades VAUDREUILLE FR	Ouvrage: Implantation de 6 HLL démontables Zone Ntc	Adresse du projet: 455 Chemin de Lasprades 31250 VAUDREUILLE
Références: section ZI parcelle 18 Date :06/07/2026	Planche: PLAN DE SITUATION	Echelle : N° de plan: DPC1

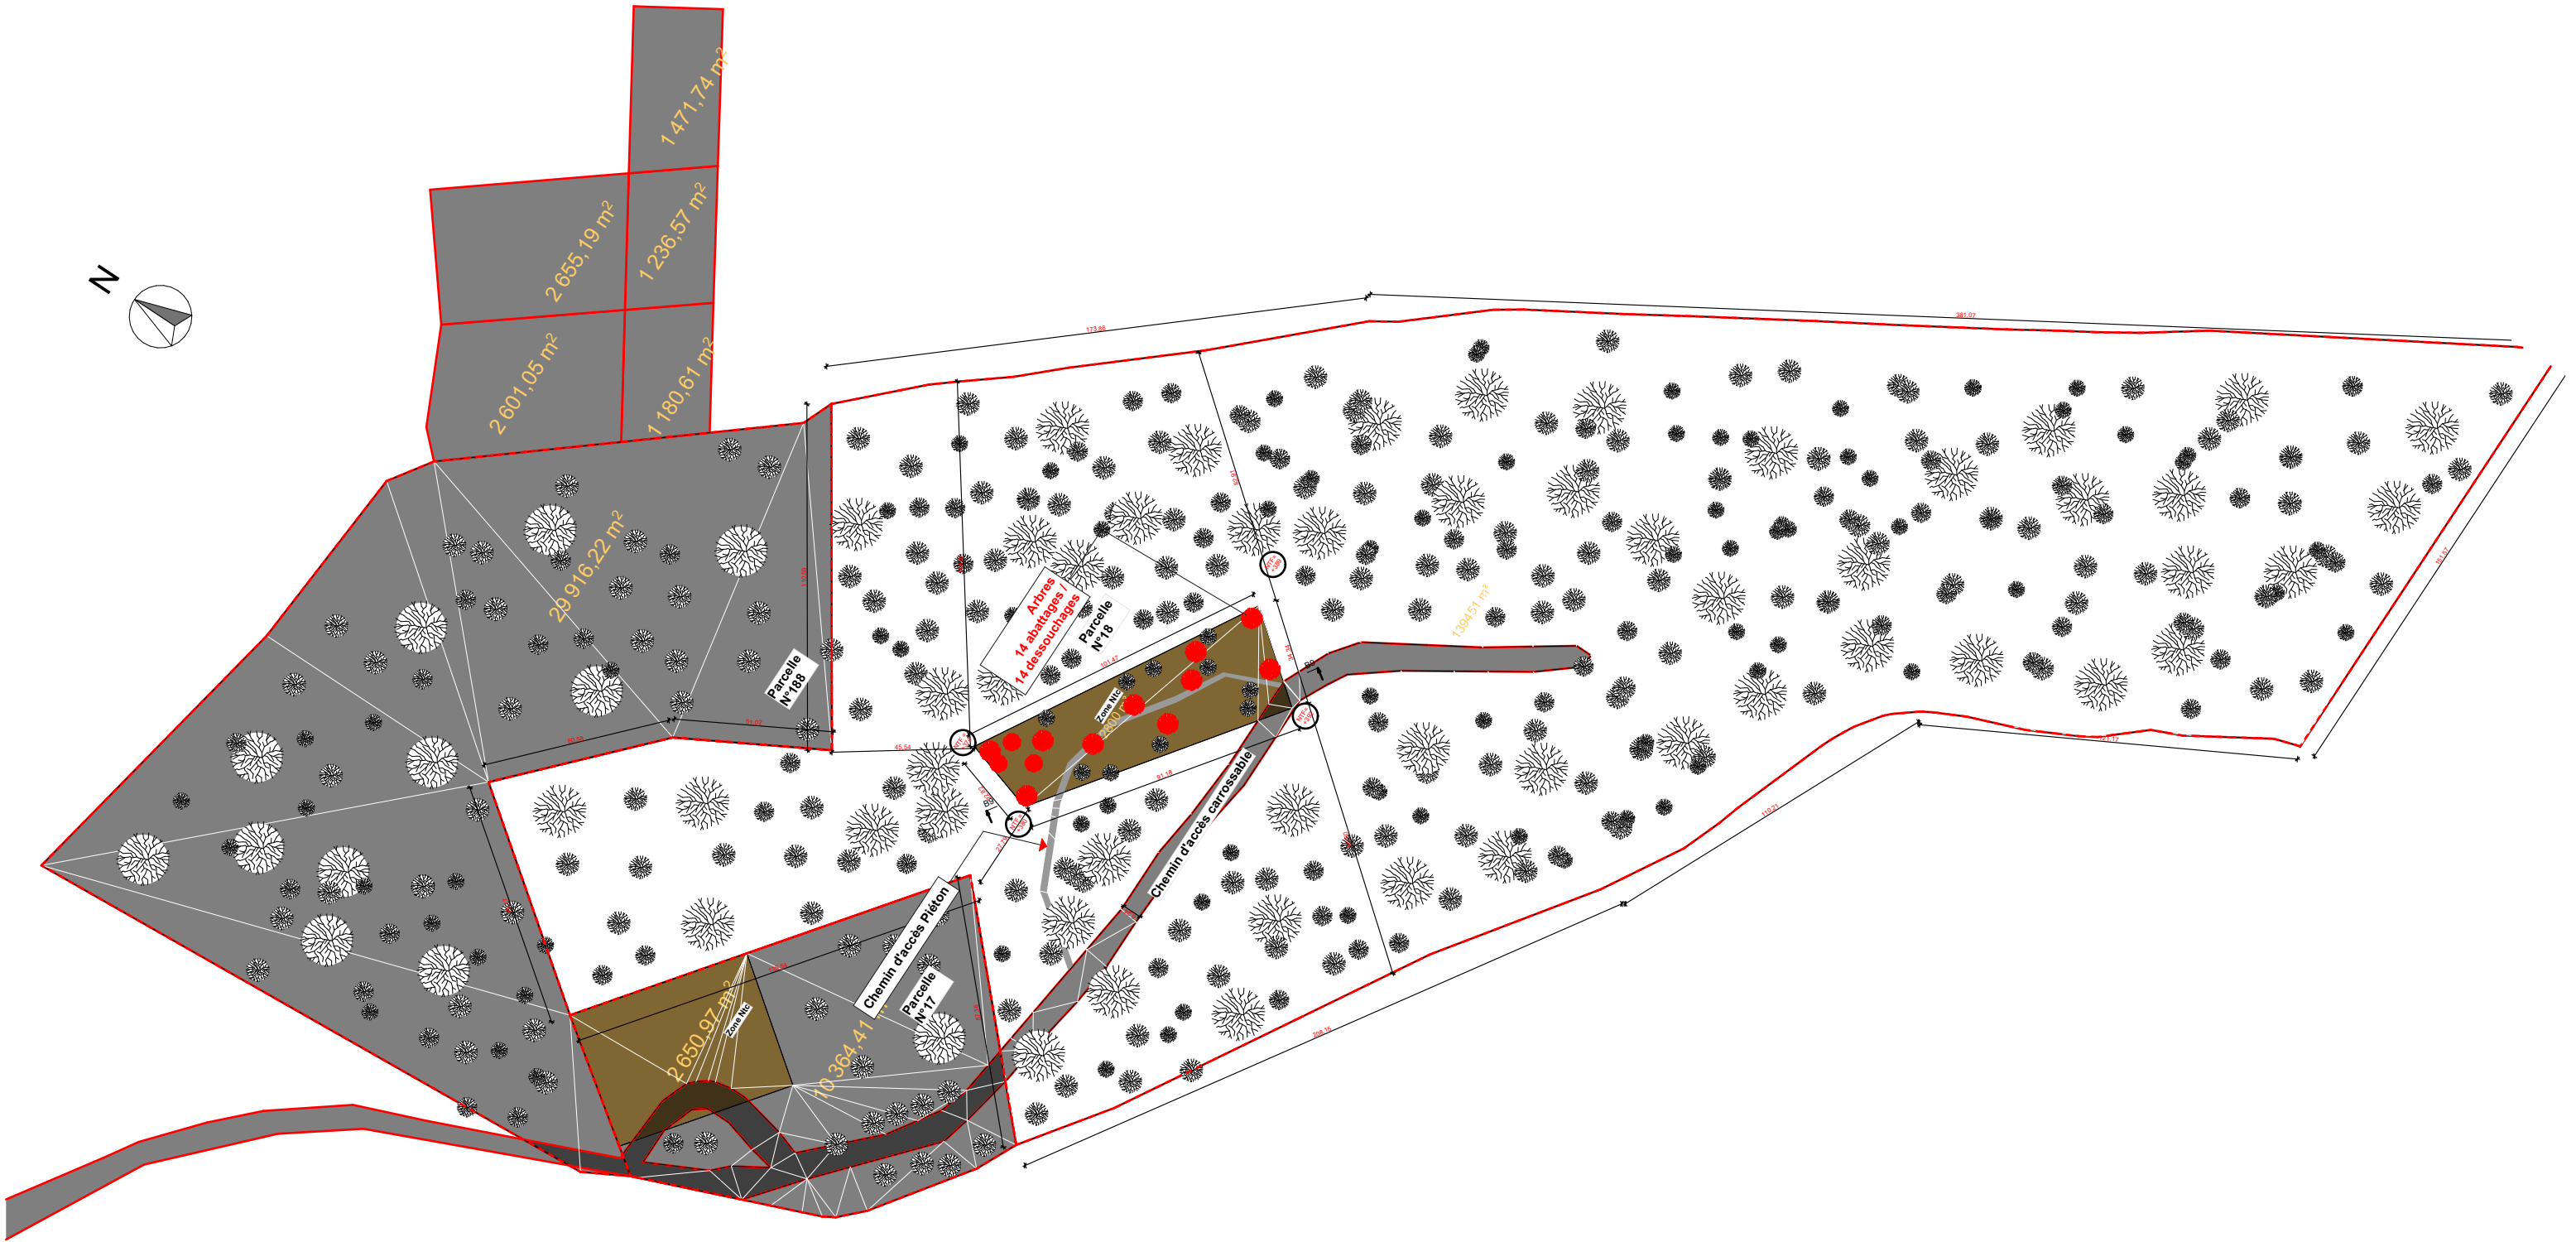

PLAN
MASSE

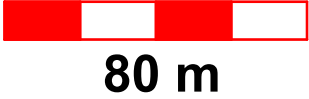


Références: section ZI parcelle 18 Date :06/07/2026	Ouvrage: Implantation de 6 HLL démontables Zone Ntc		Adresse du projet: 455 Chemin de Lasprades 31250 VAUDREUILLE
	Planche: Plan de masse général edl dans la parcelle ZI n°18	Echelle : 1:2000 N° de plan: DPC2a	

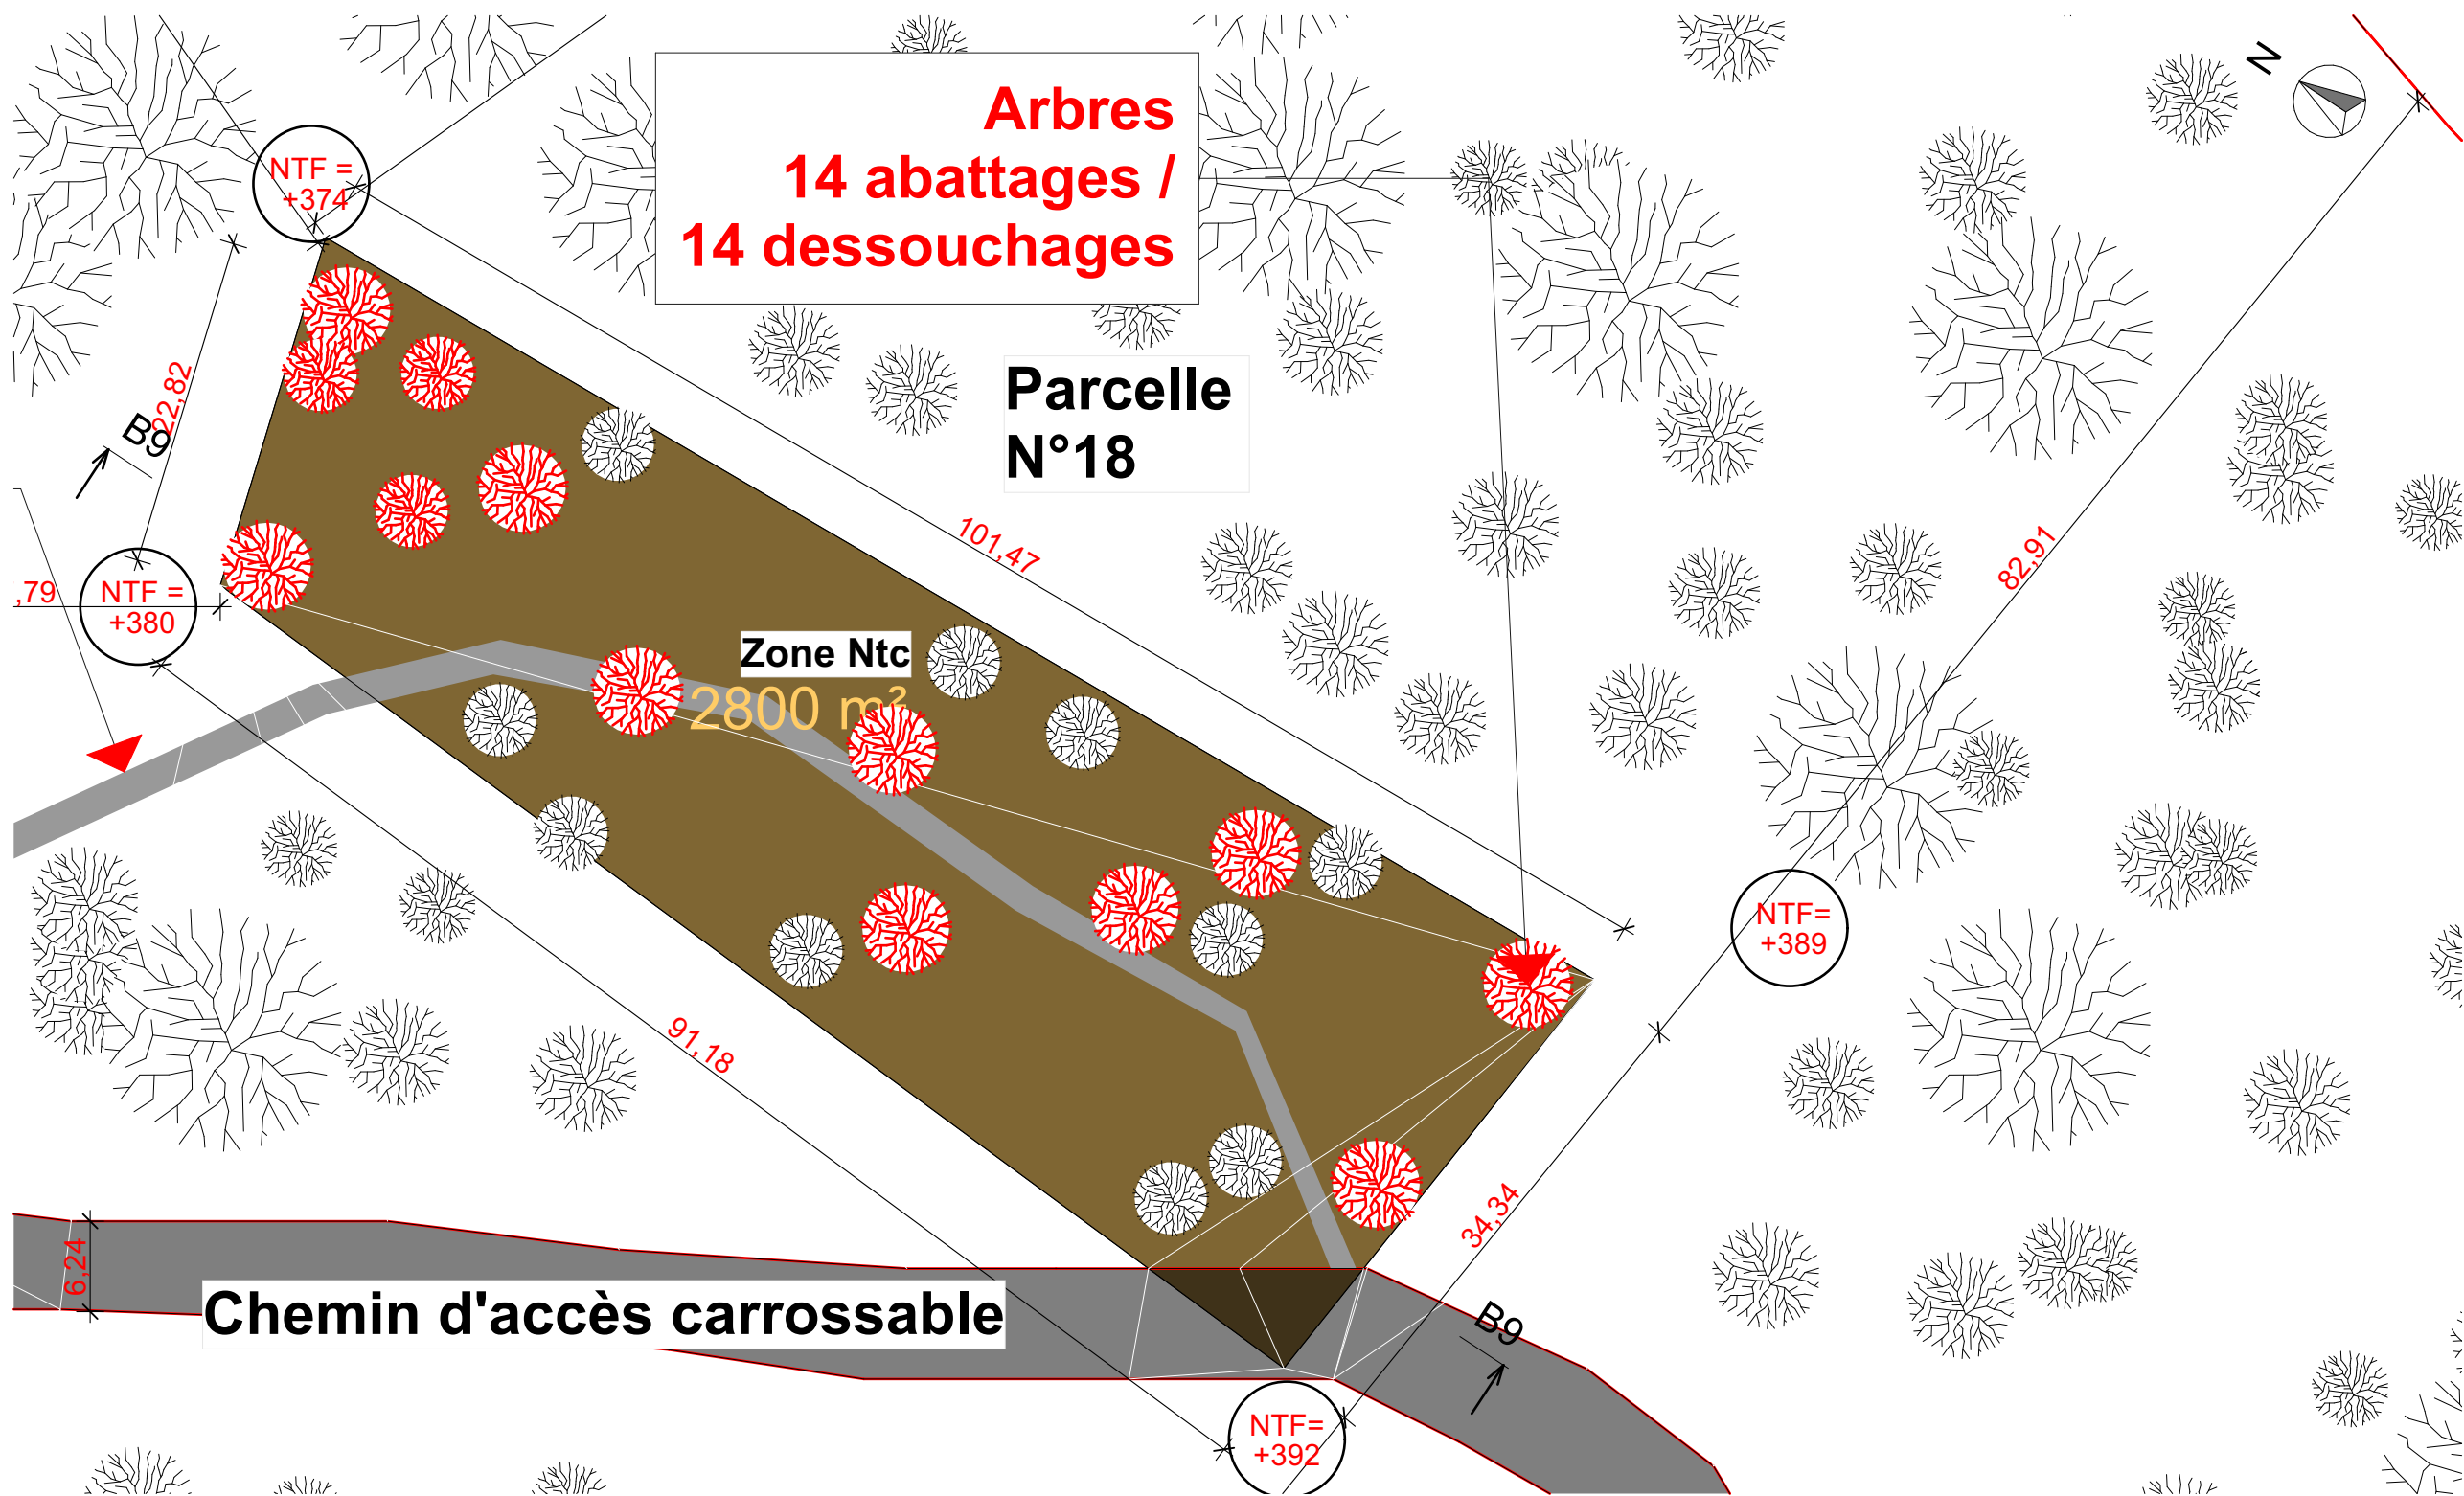

**PLAN
MASSE**



Maitre d'ouvrage: NICOLAS RABOT 455 Chemin de Lasprades VAUDREUILLE FR	Ouvrage: Implantation de 6 HLL démontables Zone Ntc	Adresse du projet: 455 Chemin de Lasprades 31250 VAUDREUILLE
Références: section ZI parcelle 18 Date :06/07/2026	Planche: Plan de masse état des lieux coté	Echelle : 1:500
		N° de plan: DPC2b

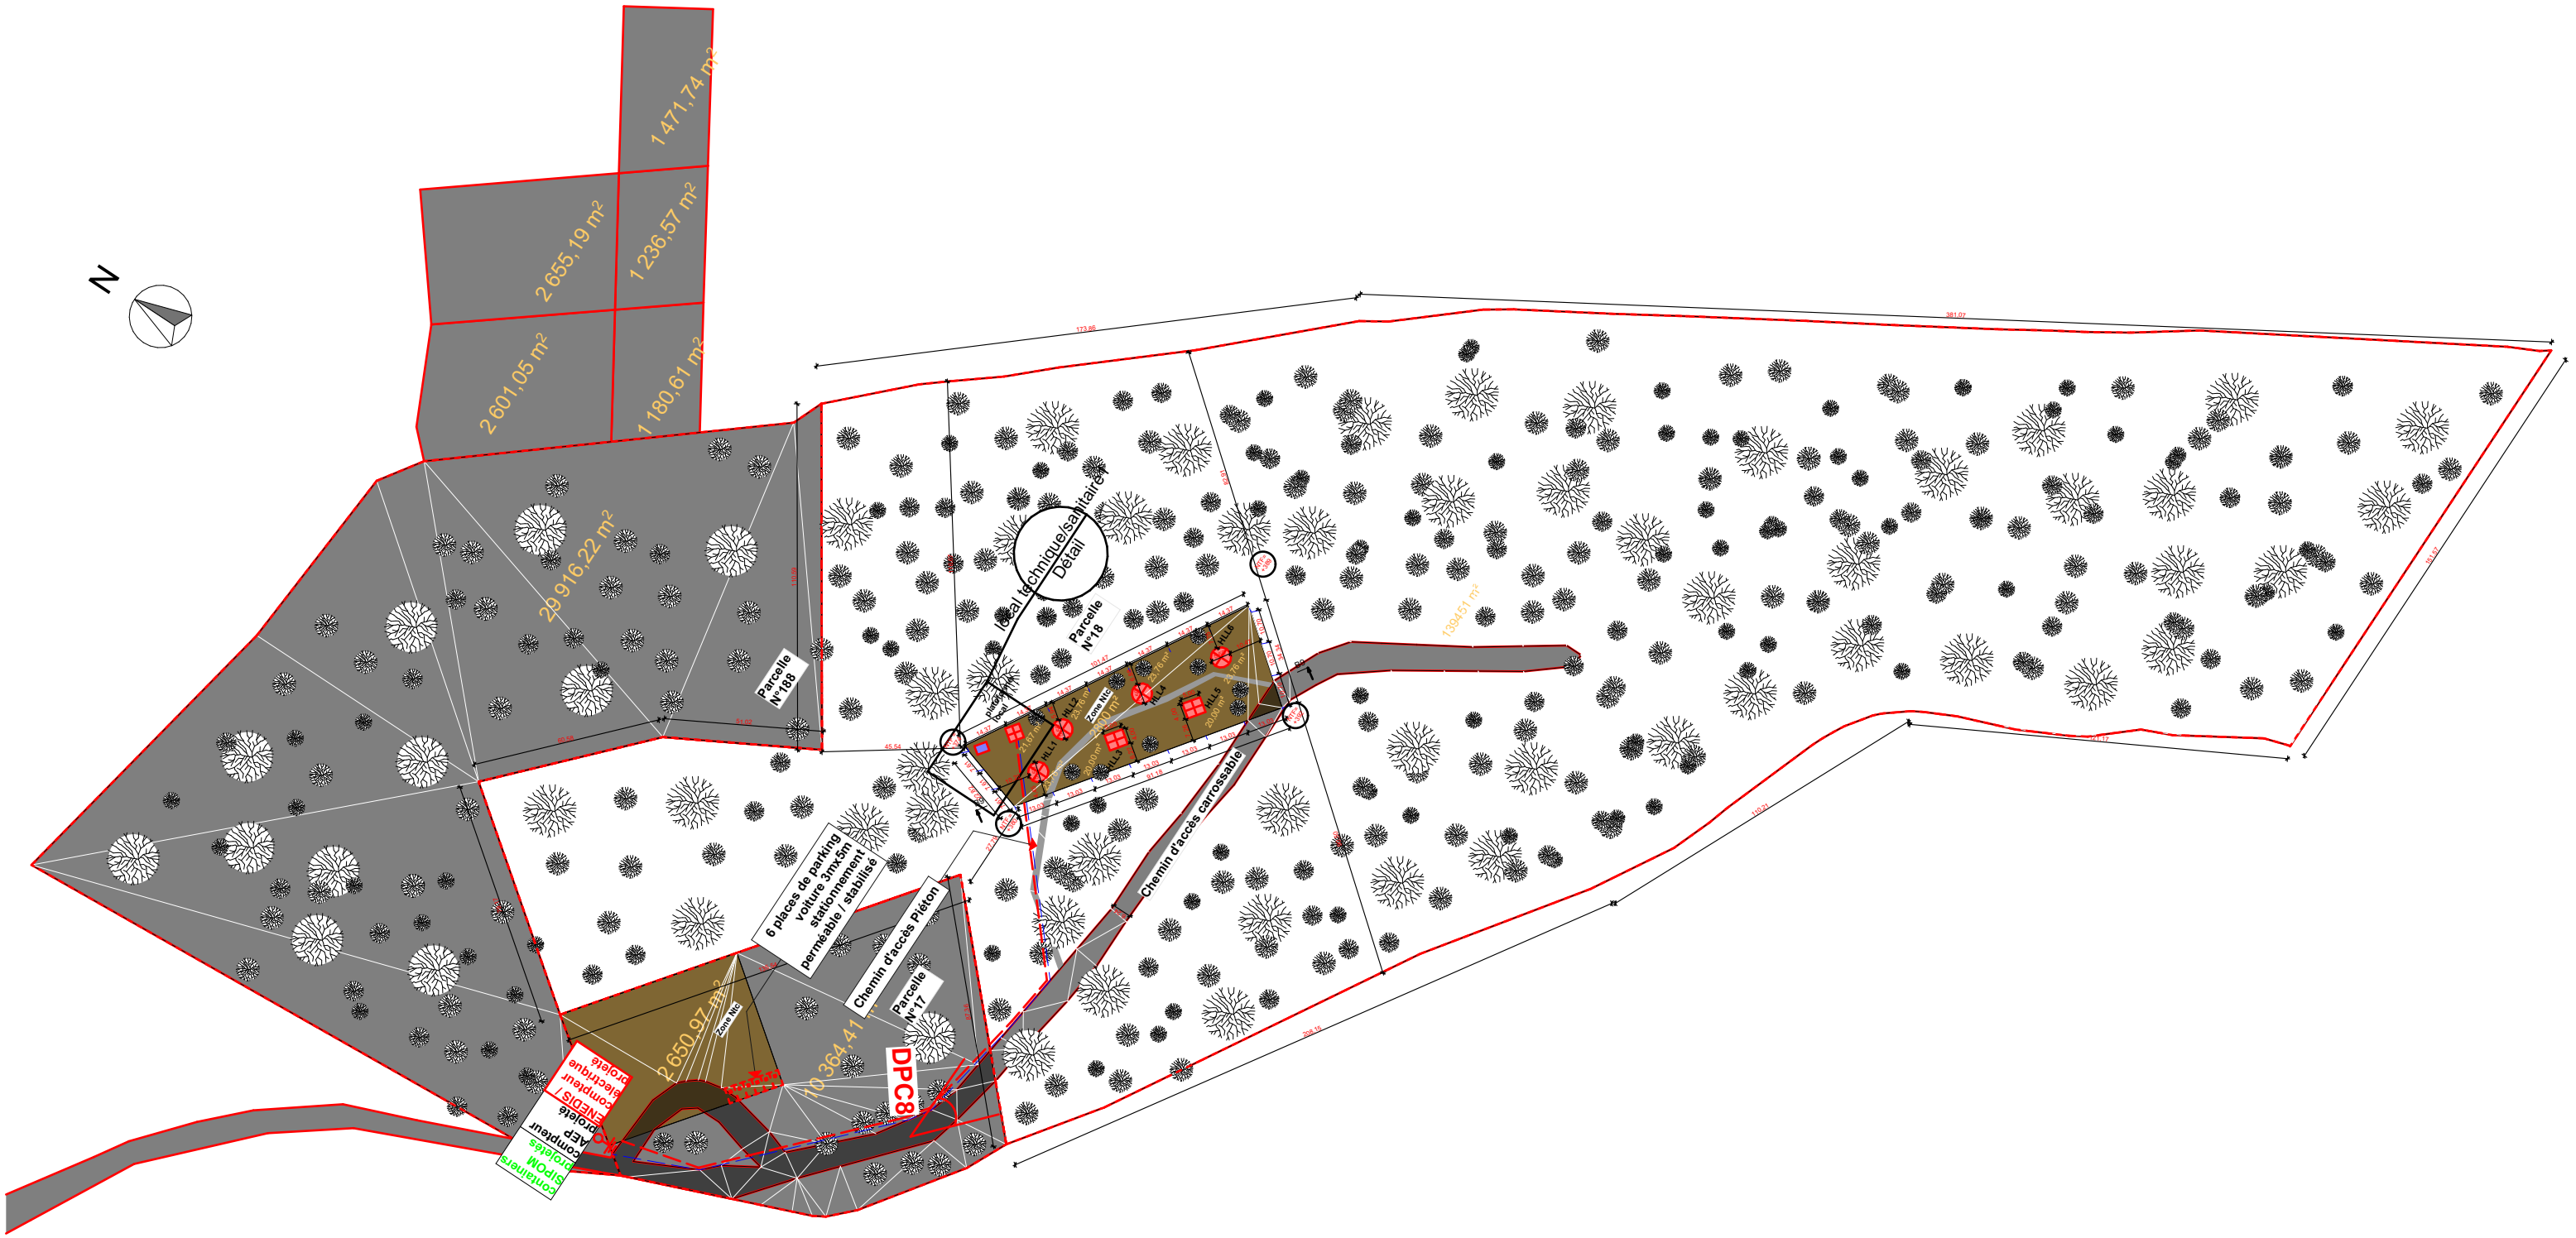


PLAN MASSE



- HLL
- électricité
- eau potable
- cheminement carrossable
- cheminement piéton
- stationnement
- assainissement

Maitre d'ouvrage: NICOLAS RABOT 455 Chemin de Lasprades VAUDREUILLE FR		Ouvrage: Implantation de 6 HLL démontables Zone Ntc	Adresse du projet: 455 Chemin de Lasprades 31250 VAUDREUILLE
Références: section ZI parcelle 18 Date :06/07/2026		Planche: Plan de masse général projet dans la parcelle ZI n°18	Echelle : 1:2000 N° de plan: DPC2c

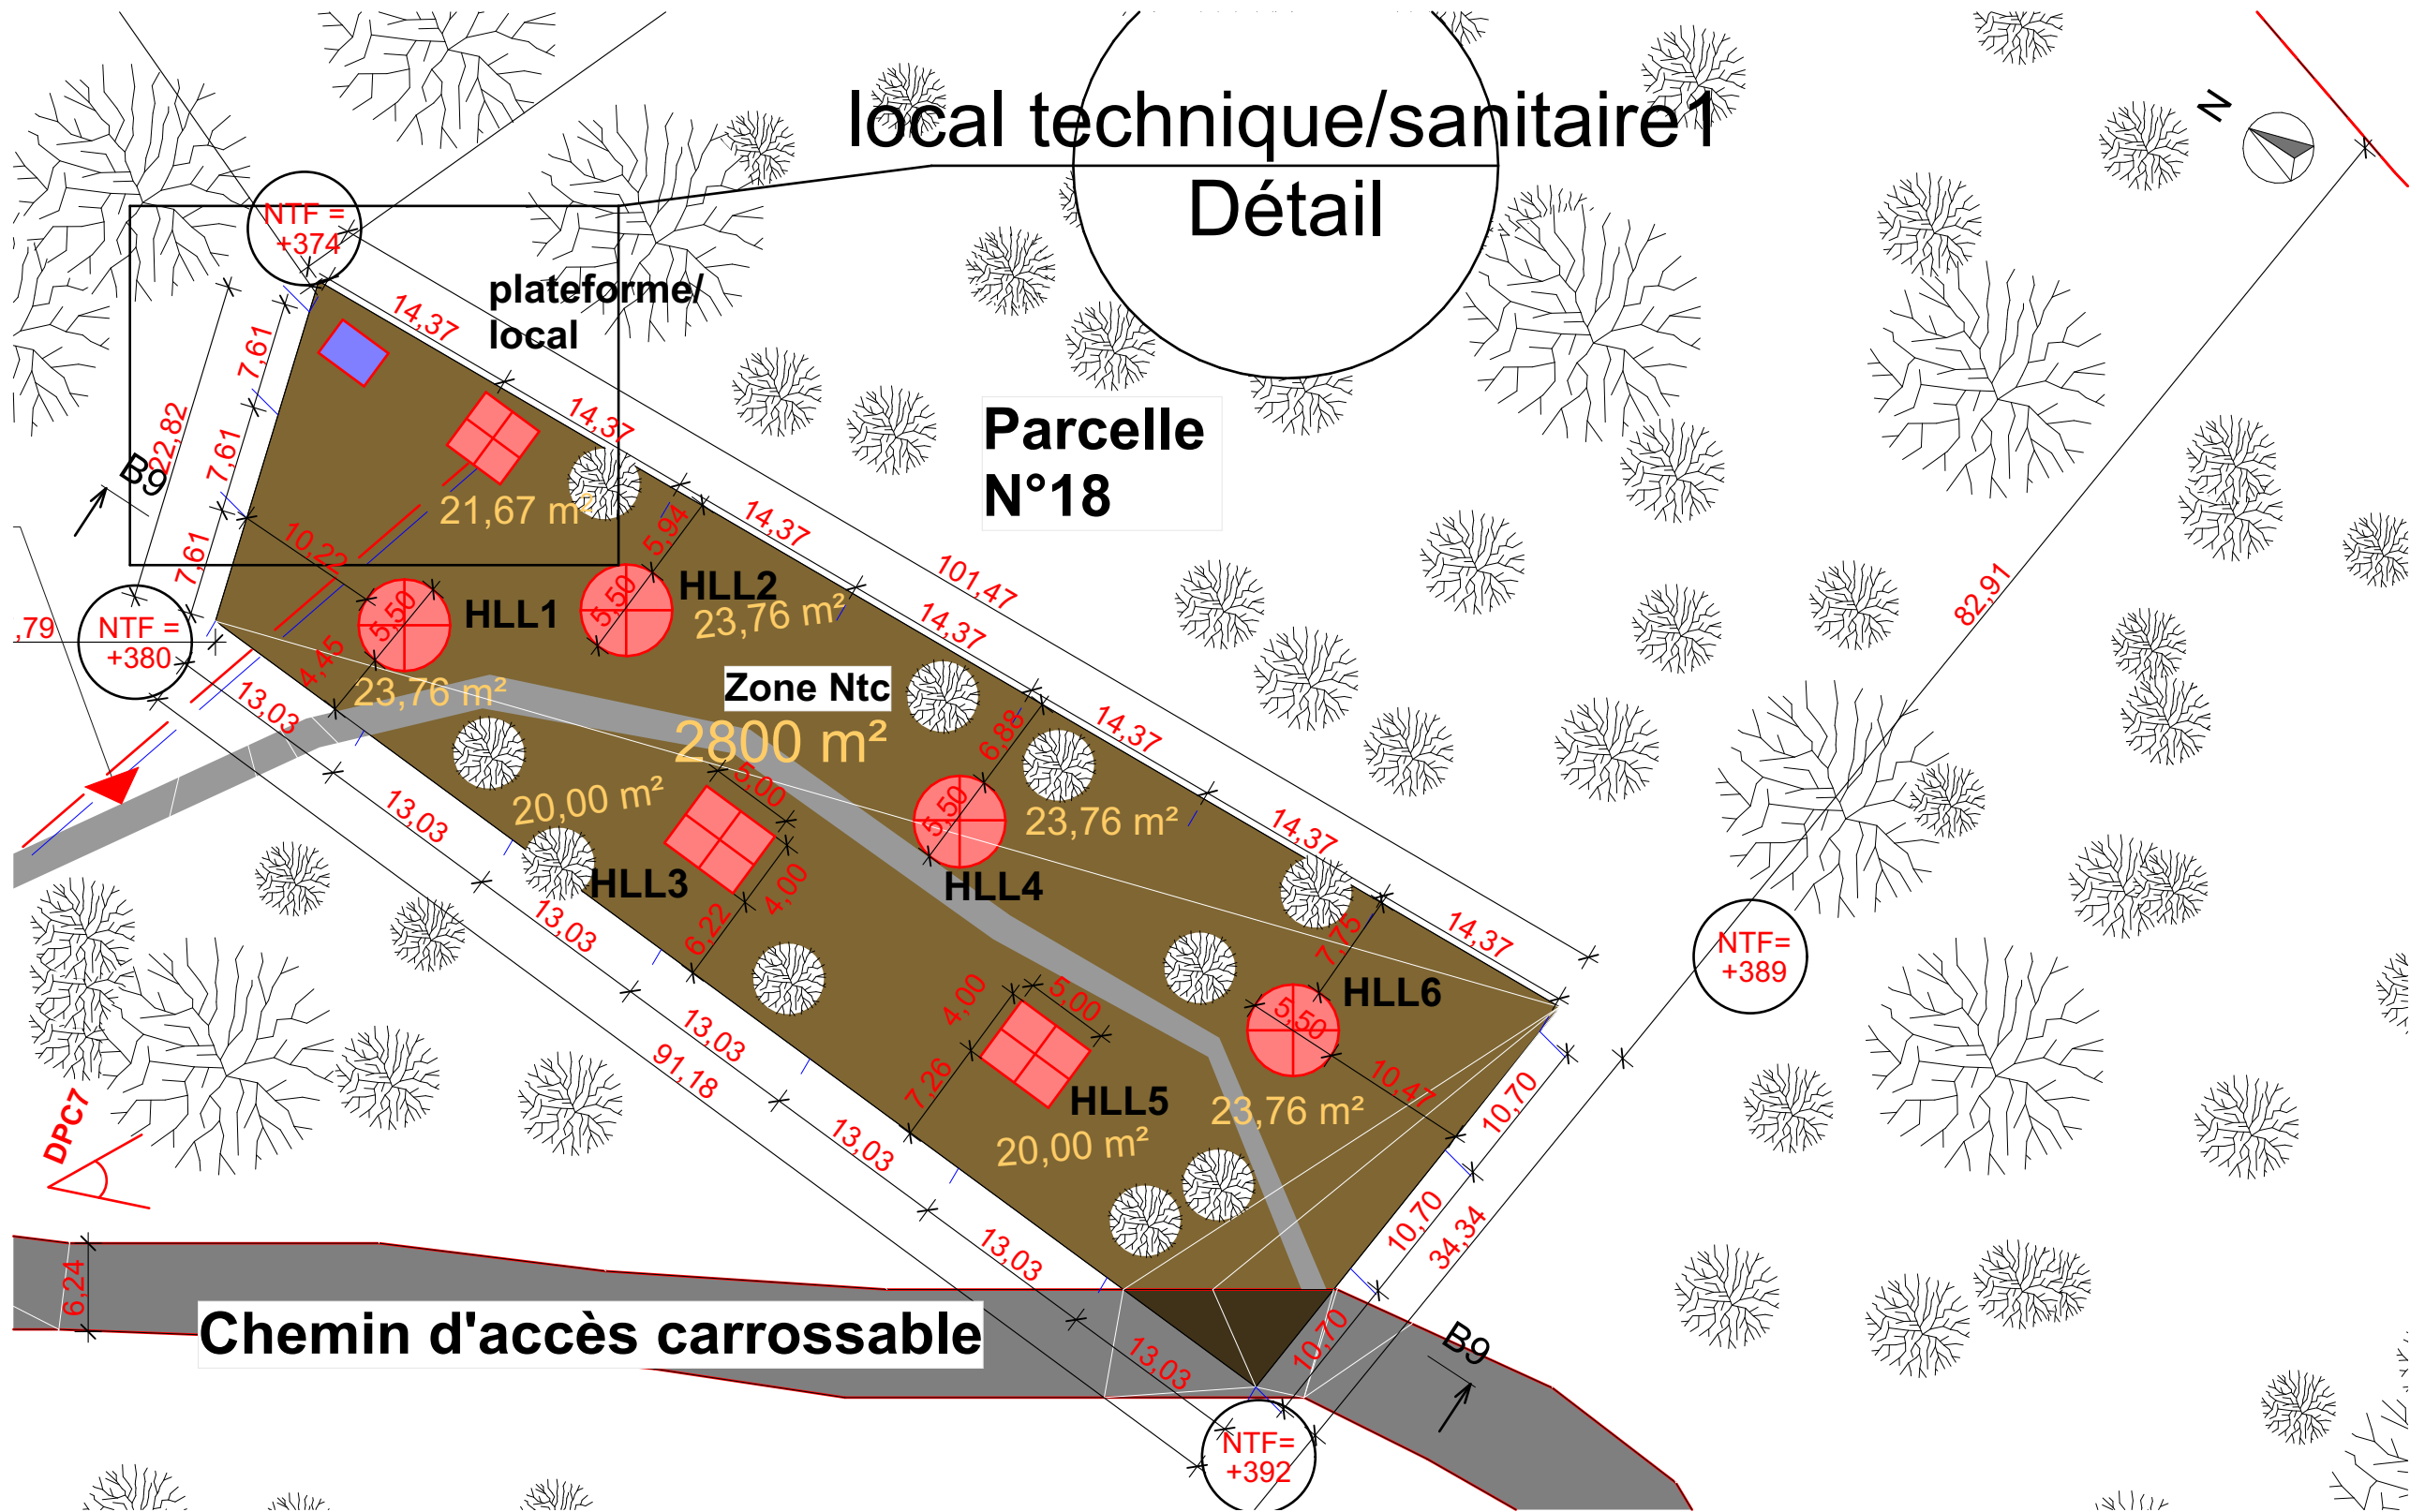


Tipi : principe tripode + perches + toile, montage/démontage (manuel de montage).
Yourte/ger : mur en treillis (khana) + perches (uni) vers couronne (toono), couverture textile.
Les cabanes sont conçues comme des structures légères démontables en panneaux (ossature bois), préfabriqués en atelier et assemblés sur site par boulonnage. Les planchers sont portés par une structure réversible hors-sol (pieux bois ou pieux vissés métalliques selon étude d'exécution), sans béton et sans fondations maçonnées. L'enveloppe est en bardage bois ventilé; la couverture est légère (bac acier isolé ou équivalent)
Projet limité à l'implantation de six habitations légères de loisirs démontables à usage touristique saisonnier.
Aucune création de terrain de camping.
Aucun emplacement nu pour tente, caravane ou camping-car n'est créé.
Stationnement léger prévu en partie basse du terrain, représenté sur le plan DPC2c.
Implantations sur planchers bois et appuis réversibles, sans fondations maçonnées ni scellement béton.

HLL 01= Tipi 5.50 m de diam ht 5.60 m sur plancher bois
HLL 02= Yourte 5.50 m de diam ht 3.90 m sur plancher bois
HLL 03= Cabane 5*4 m ht 3.80m au faitage 15 % de pente sur plancher bois
HLL 04= Tipi 5.50 m de diam ht 5.60 m sur plancher bois
HLL 05= Cabane 5*4 m ht 3.80m au faitage 15 % de pente sur plancher bois
HLL 06= Yourte 5.50 m de diam ht 3.90 m sur plancher bois

PLAN MASSE

Maitre d'ouvrage: NICOLAS RABOT 455 Chemin de Lasprades VAUDREUILLE FR	Ouvrage: Implantation de 6 HLL démontables Zone Ntc	Adresse du projet: 455 Chemin de Lasprades 31250 VAUDREUILLE
Références: section ZI parcelle 18 Date :06/07/2026	Planche: Plan de masse projet coté des 6 HLL	Echelle : 1:500 N° de plan: DPC2d

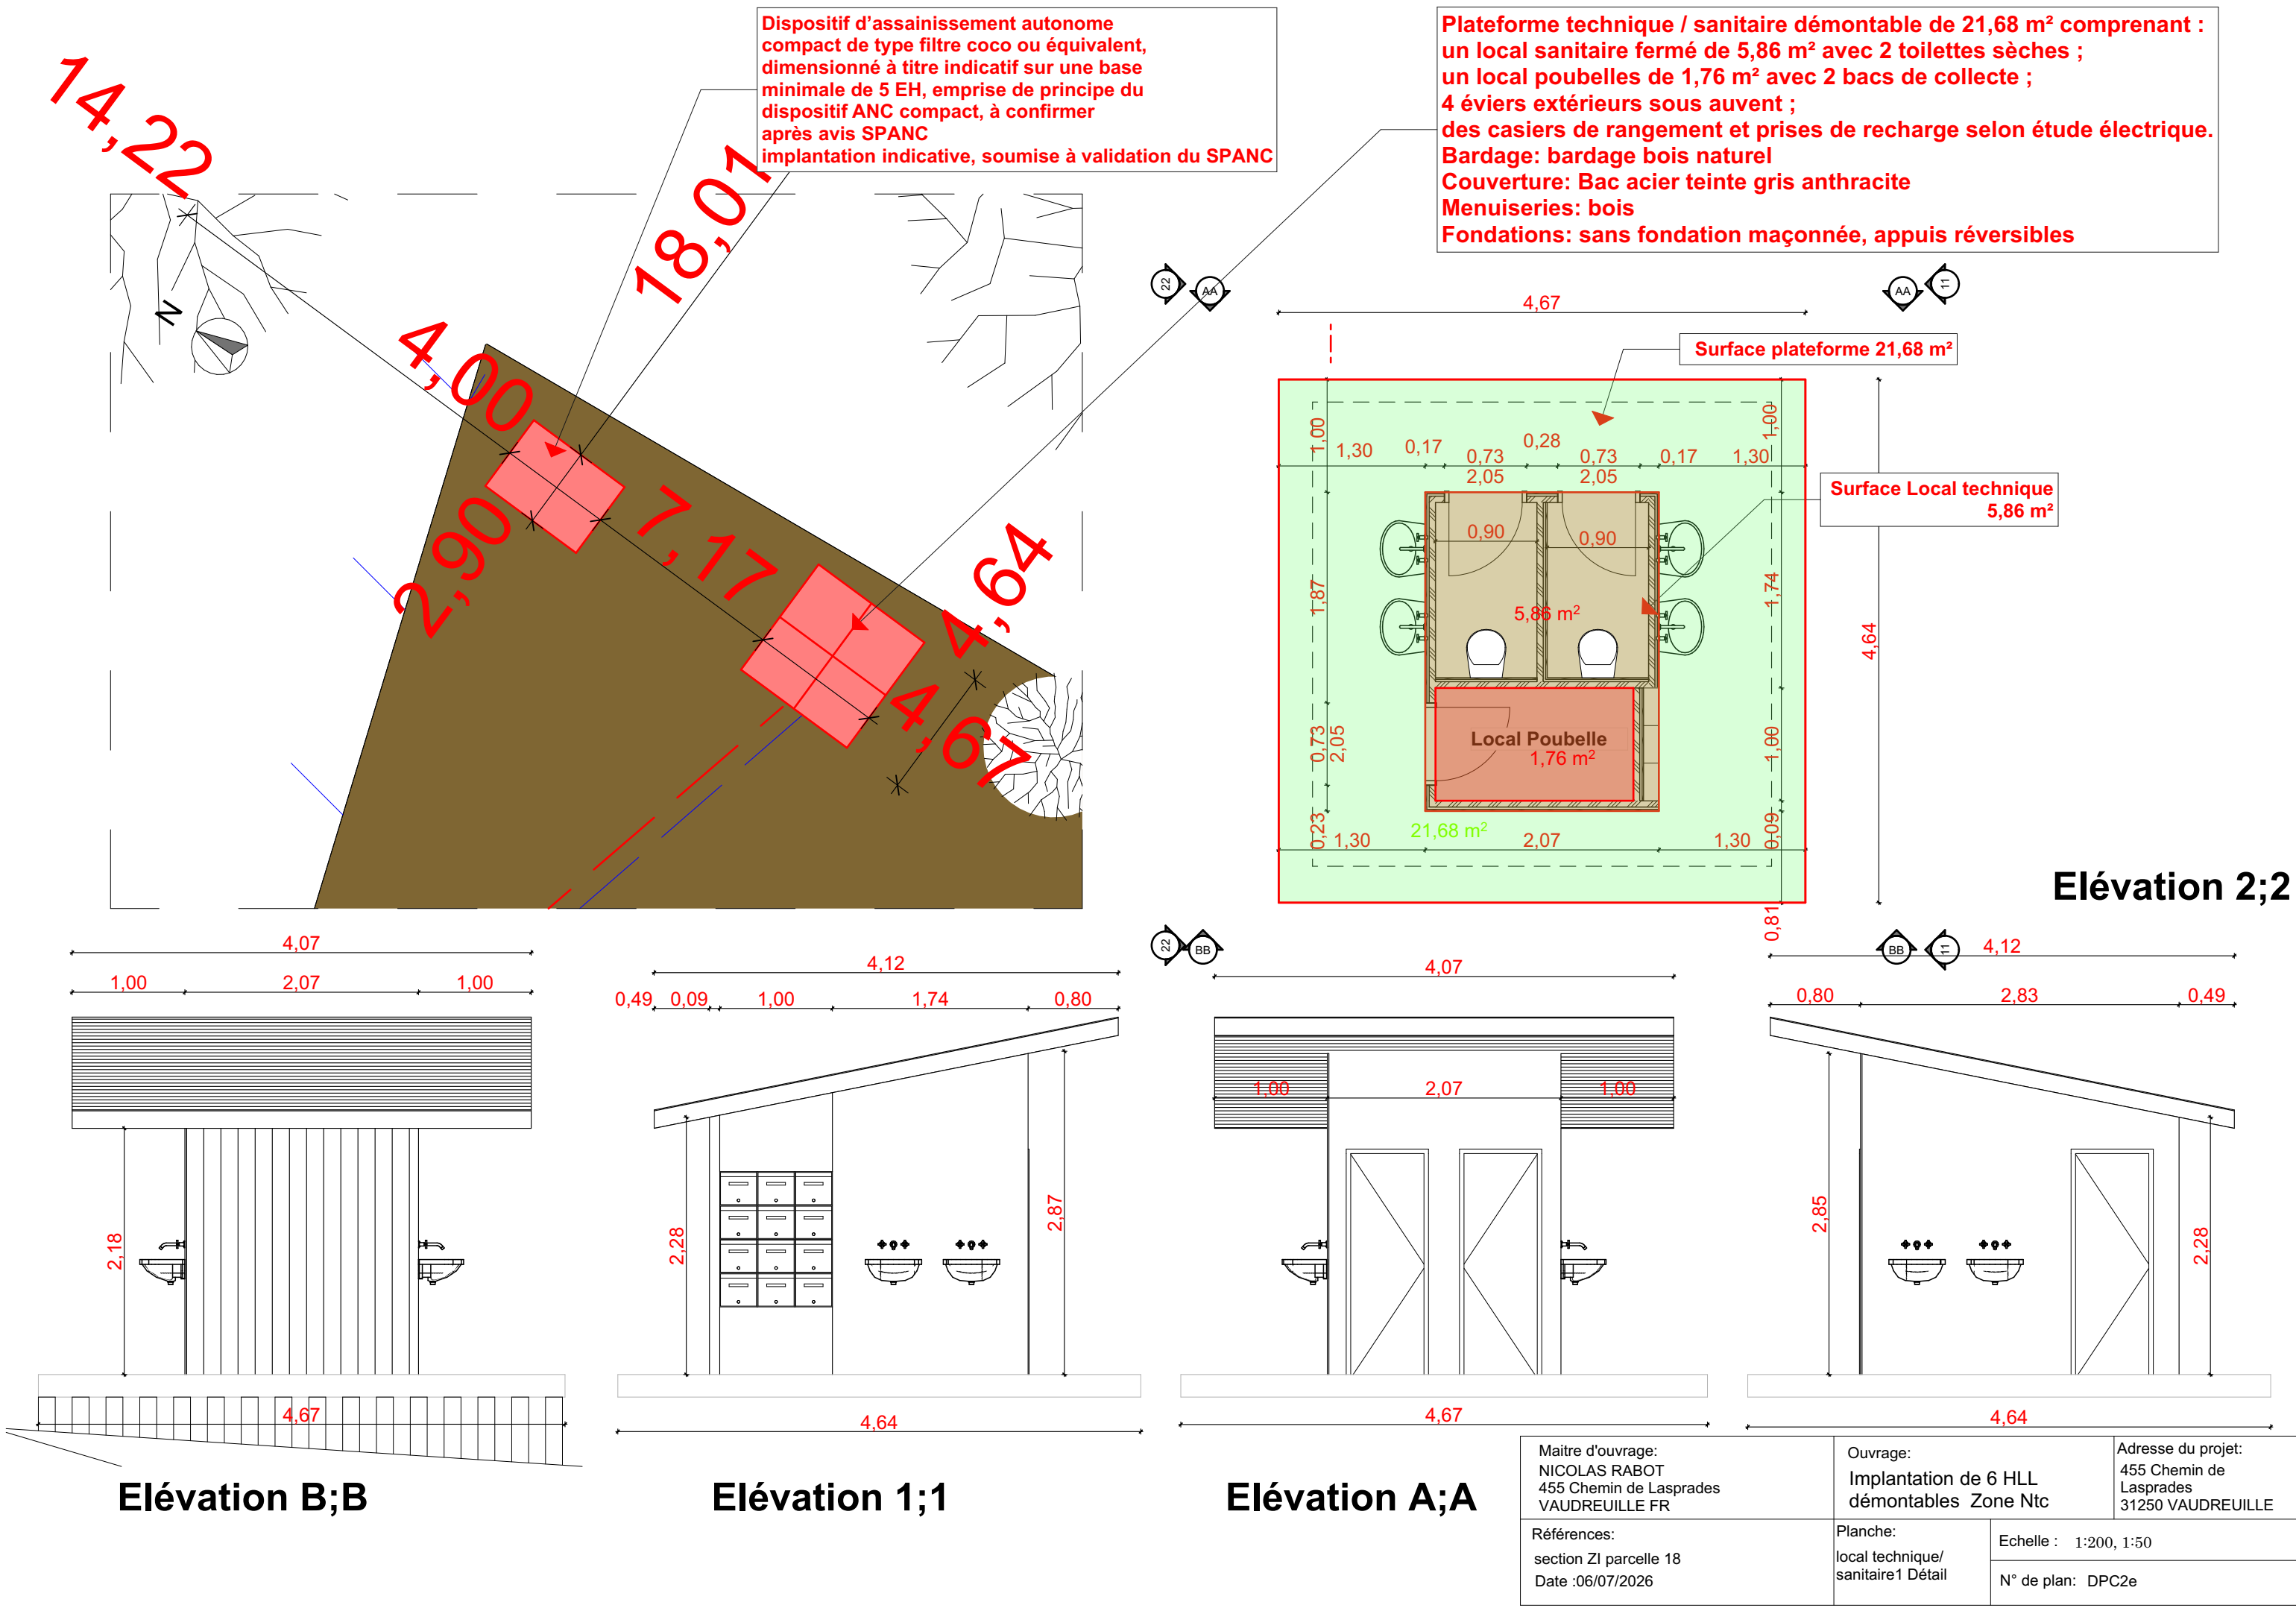

Dispositif d'assainissement autonome compact de type filtre coco ou équivalent, dimensionné à titre indicatif sur une base minimale de 5 EH, emprise de principe du dispositif ANC compact, à confirmer après avis SPANC
implantation indicative, soumise à validation du SPANC

Plateforme technique / sanitaire démontable de 21,68 m² comprenant :
un local sanitaire fermé de 5,86 m² avec 2 toilettes sèches ;
un local poubelles de 1,76 m² avec 2 bacs de collecte ;
4 évier extérieurs sous auvent ;
des casiers de rangement et prises de recharge selon étude électrique.
Bardage: bardage bois naturel
Couverture: Bac acier teinte gris anthracite
Menuiseries: bois
Fondations: sans fondation maçonnée, appuis réversibles

Surface plateforme 21,68 m²

Surface Local technique 5,86 m²

Local Poubelle 1,76 m²

Elévation 2;2

Elévation B;B

Elévation 1;1

Elévation A;A

Maître d'ouvrage:
NICOLAS RABOT
455 Chemin de Lasprades
VAUDREUILLE FR


Références:
section ZI parcelle 18
Date :06/07/2026

Ouvrage:
Implantation de 6 HLL
démontables Zone Ntc



Planche:
local technique/
sanitaire1 Détail

Echelle : 1:200, 1:50
N° de plan: DPC2e

Adresse du projet:
455 Chemin de
Lasprades
31250 VAUDREUILLE

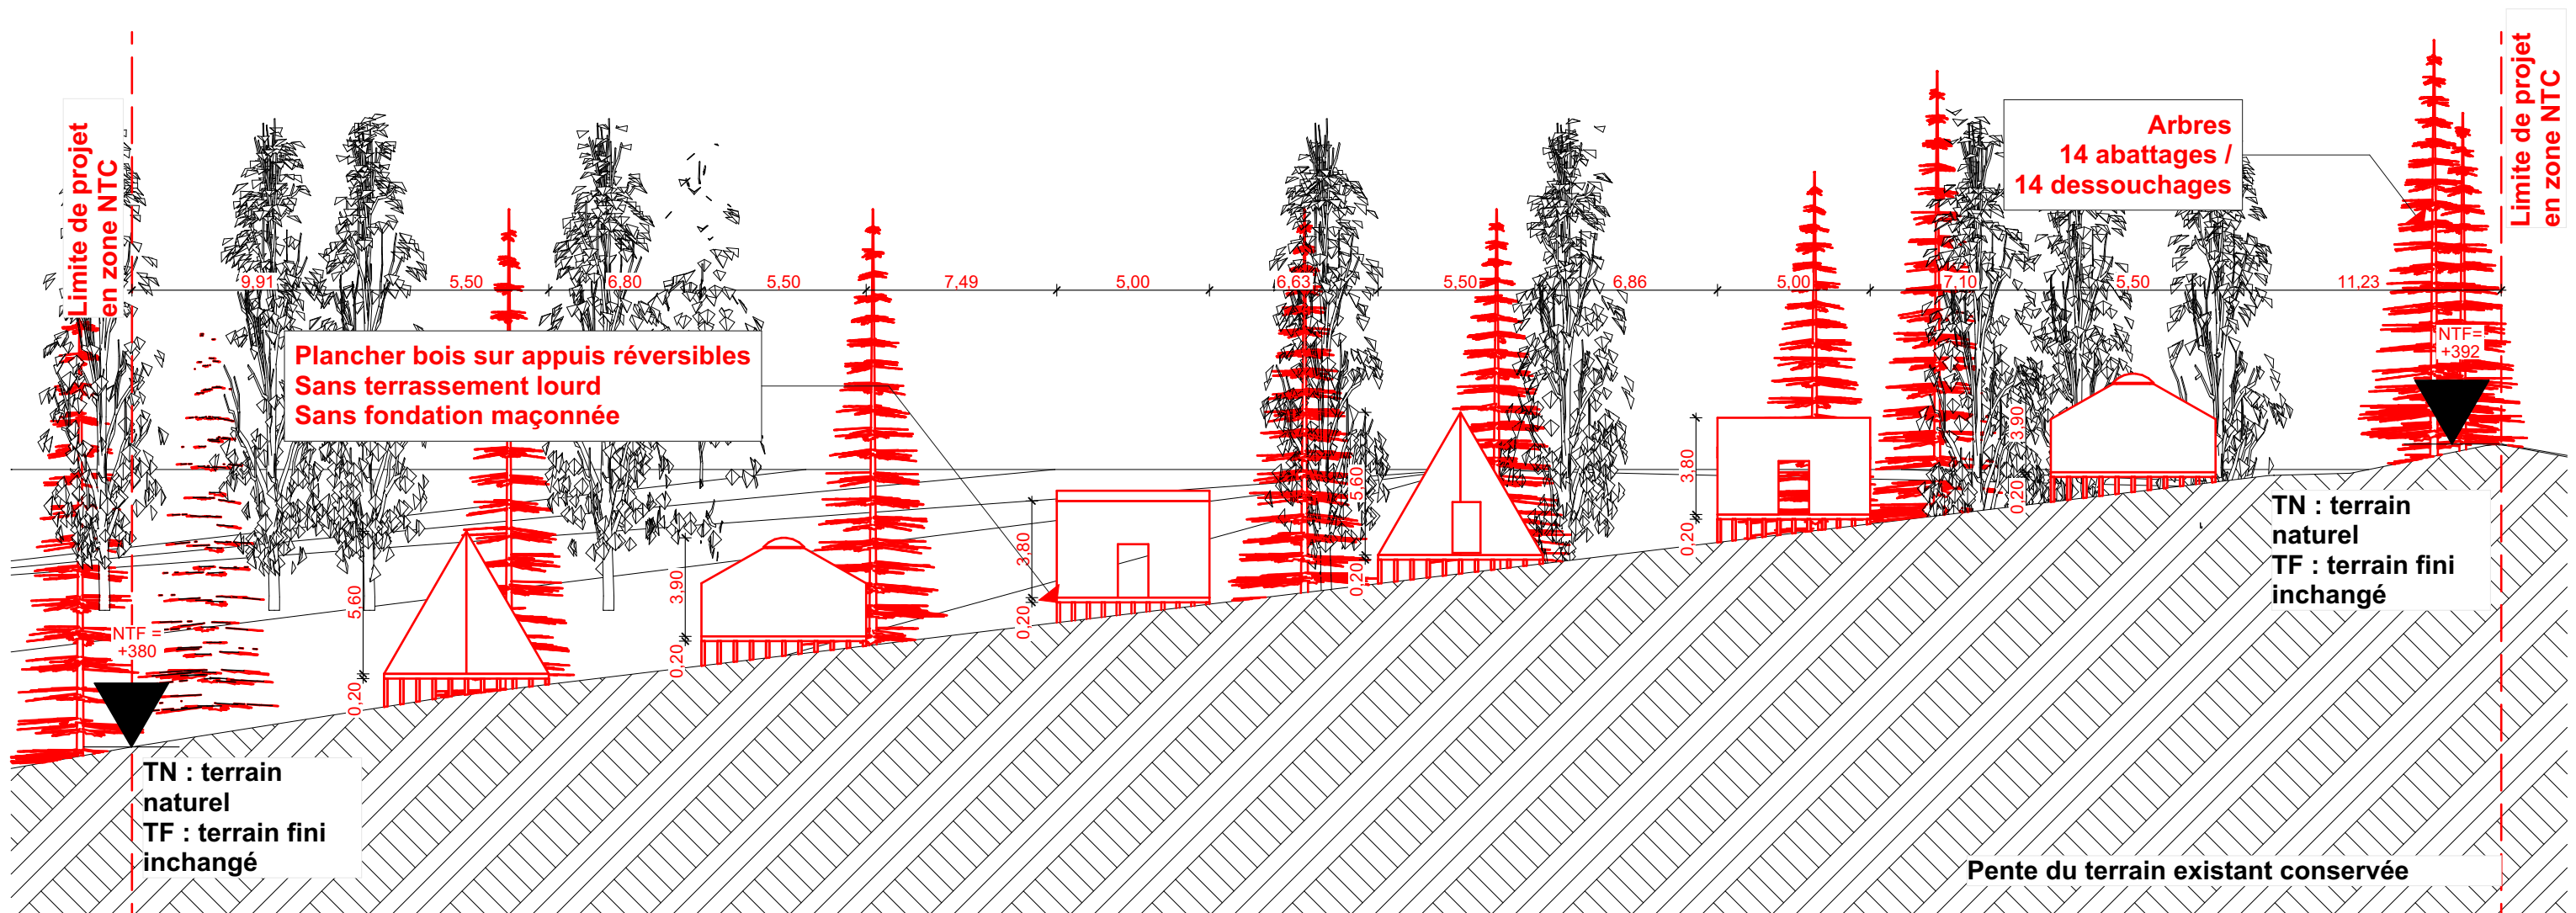

Références: section ZI parcelle 18 Date :06/07/2026	Maitre d'ouvrage: NICOLAS RABOT 455 Chemin de Lasprades VAUDREUILLE FR	Ouvrage: Implantation de 6 HLL démontables Zone Ntc	Adresse du projet: 455 Chemin de Lasprades 31250 VAUDREUILLE
	Planche: Coupe d'implantation des HLL dans le terrain naturel	Echelle : 1:250 N° de plan: DPC3;6;7;8	

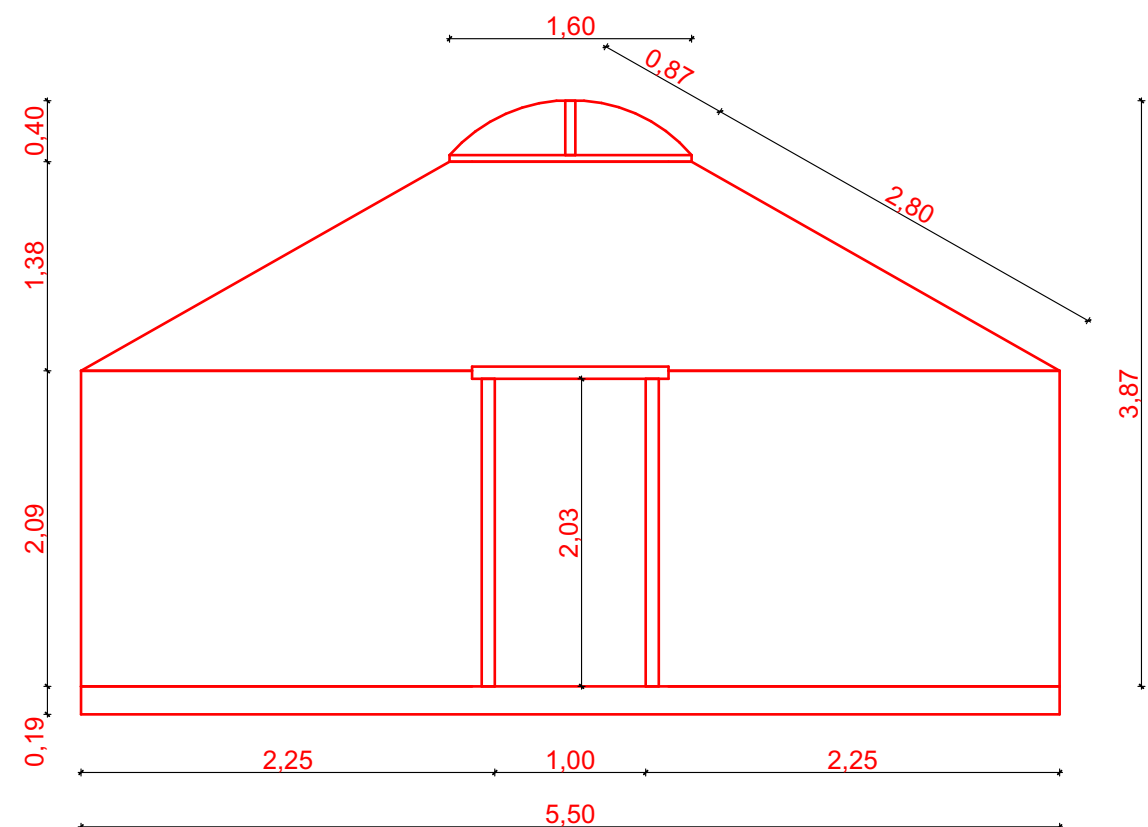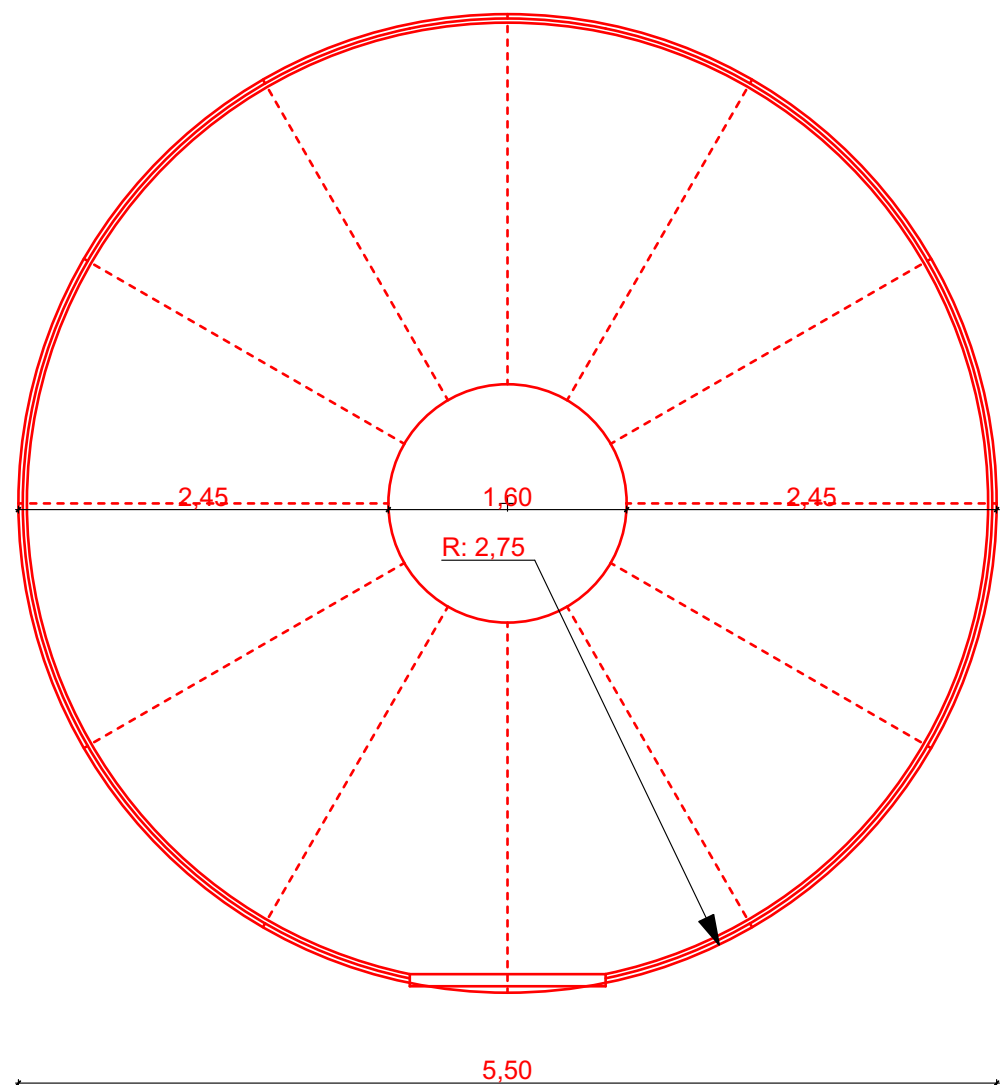



2 m



Photos d'intention

Matériaux: toile textile claire, structure bois, plancher bois
Couleurs: teinte toile beige / écru, bois naturel
Fondation: sans fondation maçonnée, appuis réversibles
Usage: usage touristique saisonnier, non permanent



Références: section ZI parcelle 18 Date :06/07/2026	Ouvrage: Implantation de 6 HLL démontables Zone Ntc		Adresse du projet: 455 Chemin de Lasprades 31250 VAUDREUILLE
	Planche: Façades / toiture HLL type Yourte	Echelle : 1:50, 1:1 N° de plan: DPC4a	

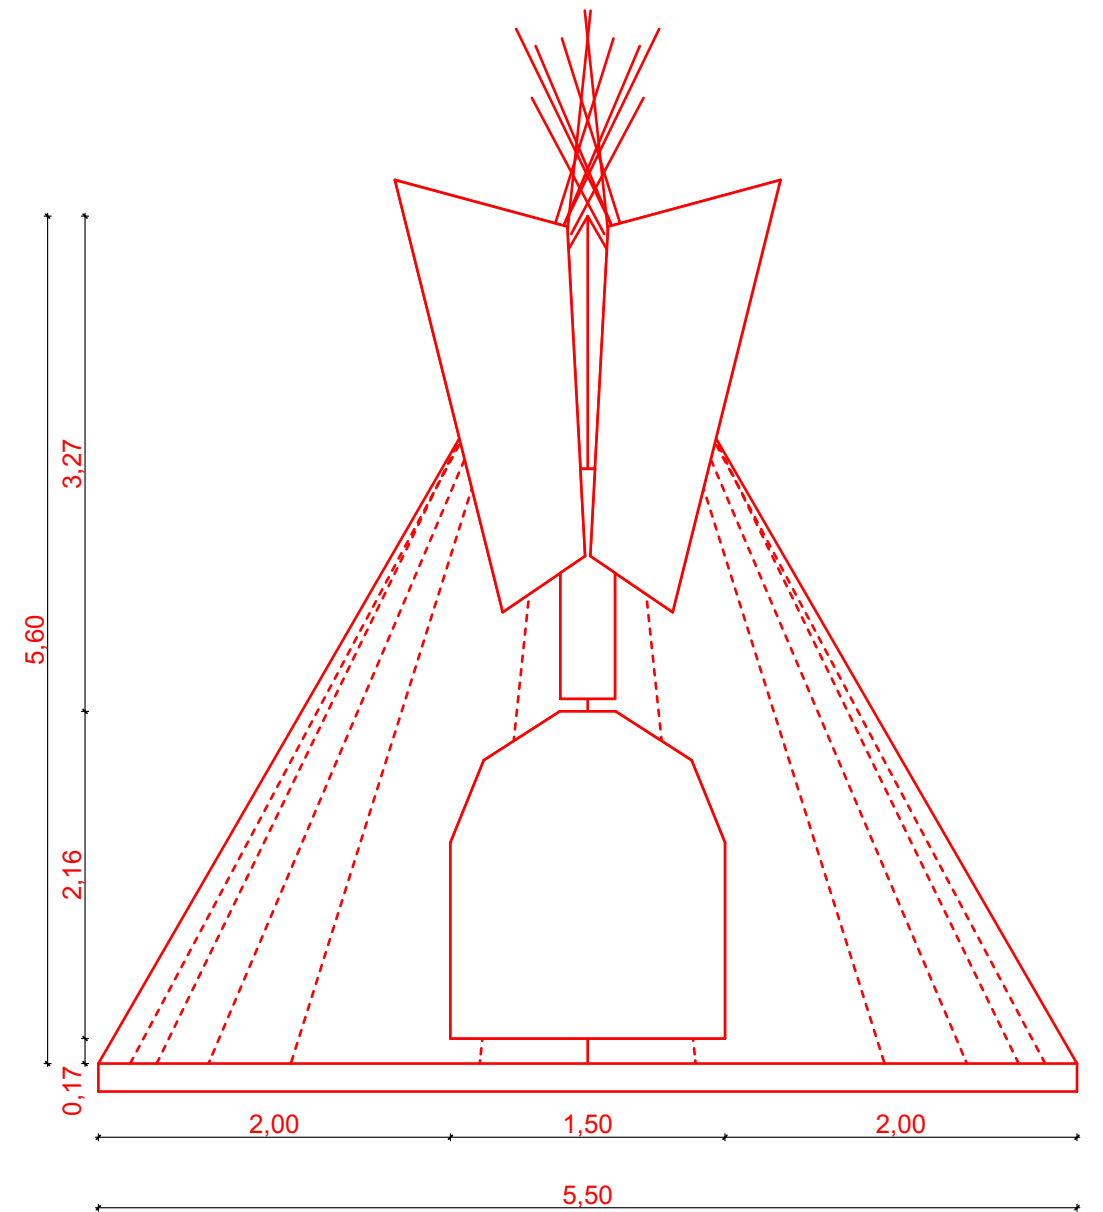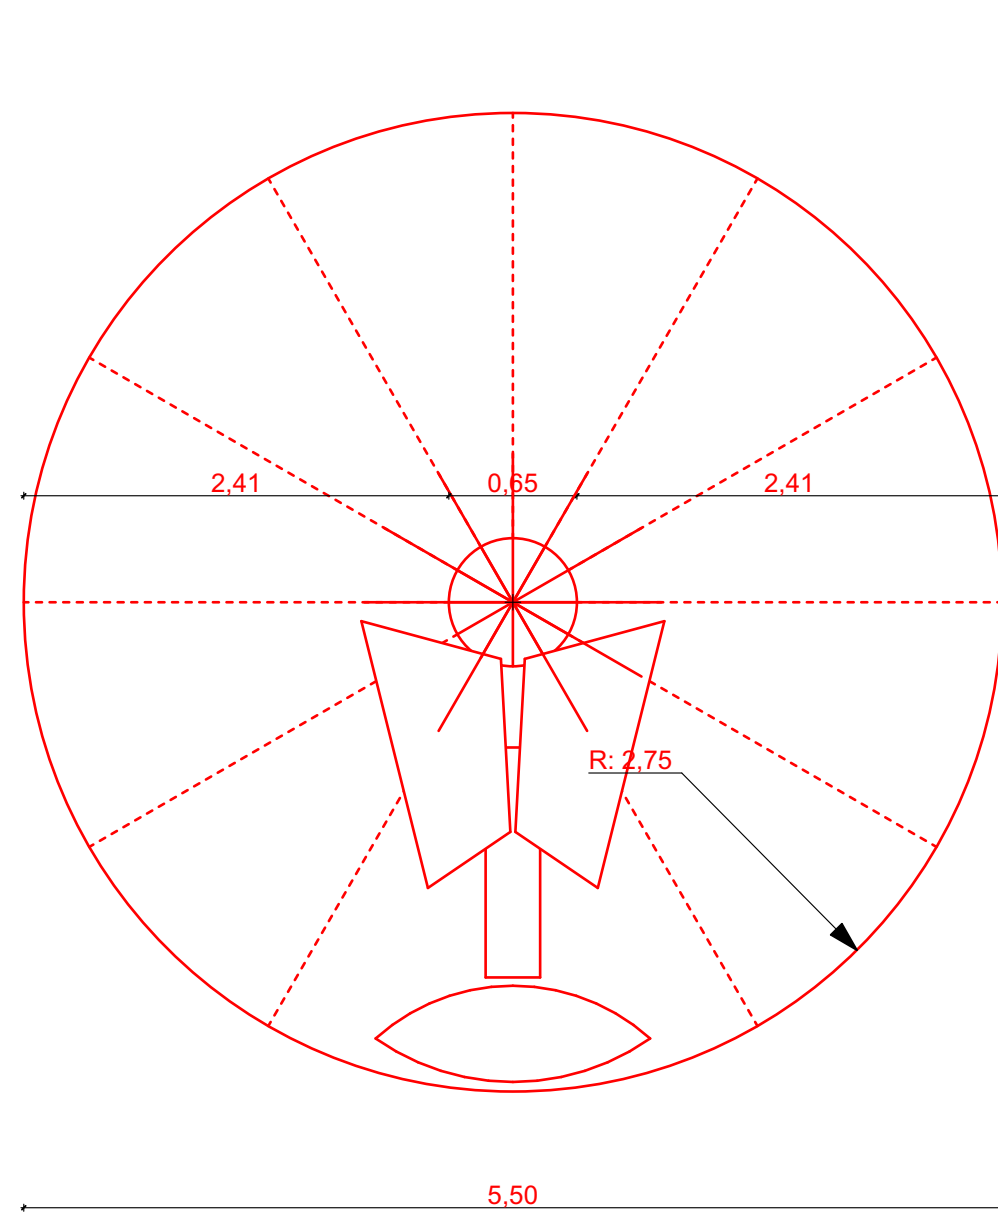

Photos d'intention


Matériaux: toile textile claire, structure bois, plancher bois
Couleurs: teinte toile beige / écru, bois naturel
structure: perches bois
Fondation: sans fondation maçonnée, appuis réversibles
Usage: usage touristique saisonnier, non permanent

Maitre d'ouvrage: NICOLAS RABOT 455 Chemin de Lasprades VAUDREUILLE FR	Ouvrage: Implantation de 6 HLL démontables Zone Ntc	Adresse du projet: 455 Chemin de Lasprades 31250 VAUDREUILLE
Références: section ZI parcelle 18 Date :06/07/2026	Planche: Façades / toiture HLL type Tipi	Echelle : 1:50, 1:4,66 N° de plan: DPC4b

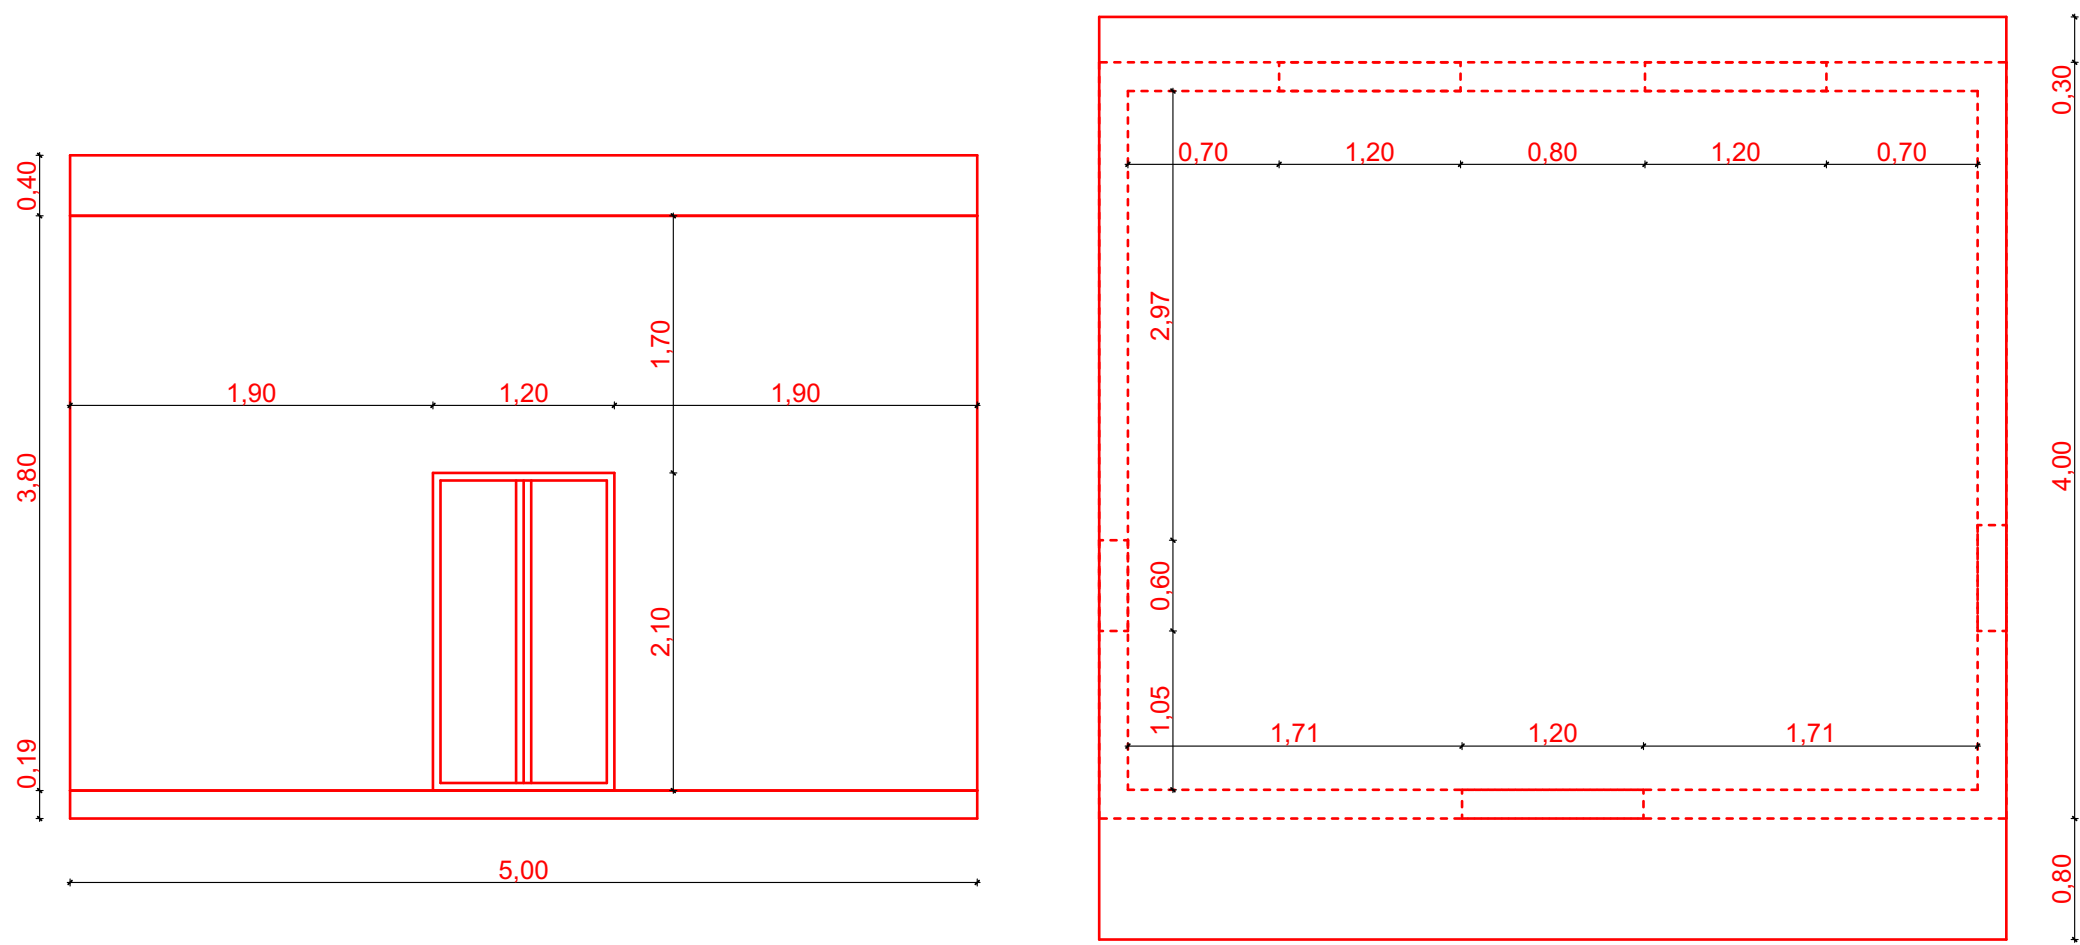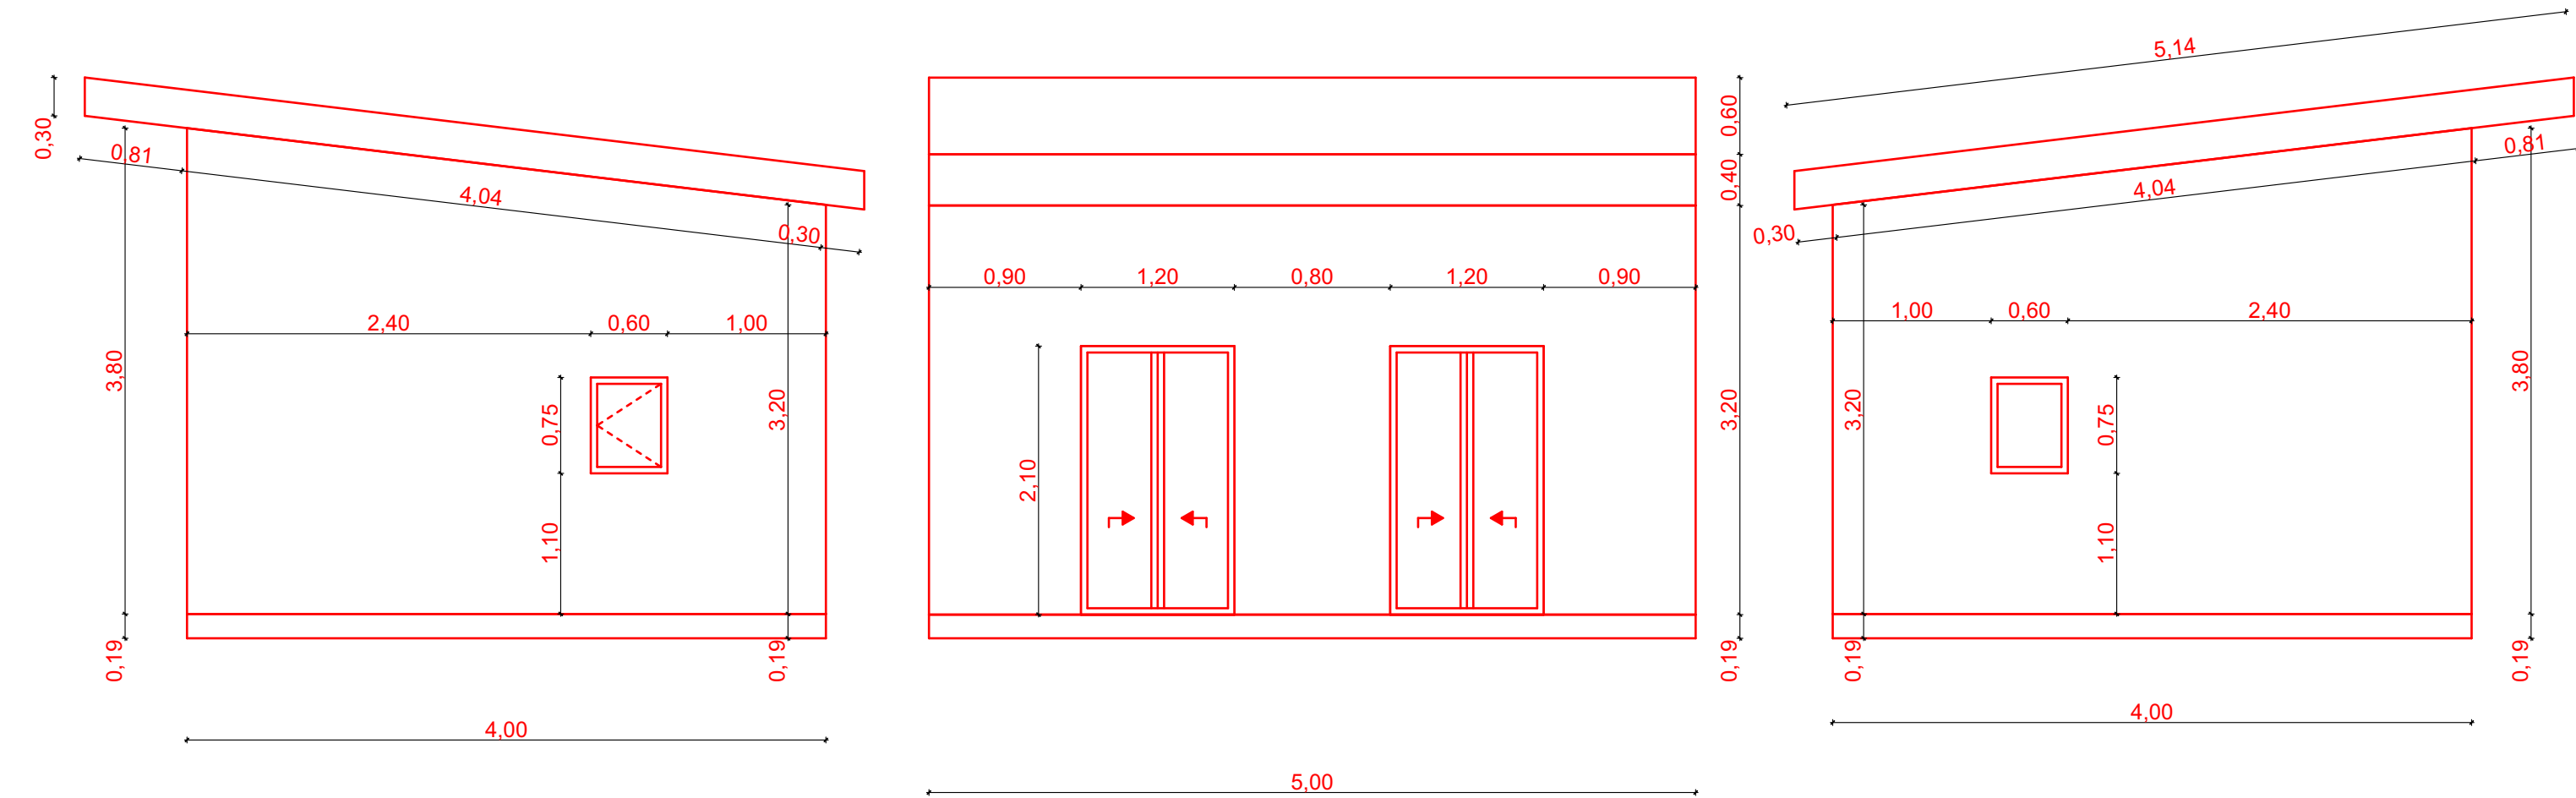

Photos d'intention

Surface déclarée de la cabane : 20,00 m²
correspondant au volume principal / plancher, hors débords légers de toiture.

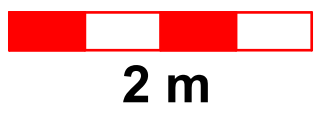

Bardage: bardage bois naturel
Couverture: Bac acier teinte gris anthracite
Menuiseries: Aluminium gris anthracite
Fondation: sans fondation maçonnée, appuis réversibles
Usage: usage touristique saisonnier, non permanent

Maitre d'ouvrage: NICOLAS RABOT 455 Chemin de Lasprades VAUDREUILLE FR	Ouvrage: Implantation de 6 HLL démontables Zone Ntc	Adresse du projet: 455 Chemin de Lasprades 31250 VAUDREUILLE
Références: section ZI parcelle 18 Date :06/07/2026	Planche: Façades / toiture HLL type Cabane	Echelle : 1:50, 1:1,33 N° de plan: DPC4c

Projet
Maître d’ouvrage :Nicolas RABOT
Adresse du projet : 455 chemin de Lasprades — 31250 Vaudreuille
Références cadastrales : section ZI — parcelle n°18
Objet de la demande :implantation de 6 habitations légères de loisirs démontables à usage touristique saisonnier, en zone Ntc.
La présente notice accompagne la déclaration préalable relative à l’implantation de six habitations légères de loisirs démontables, réparties comme suit :
- 2 tipis démontables sur plancher bois ;
- 2 yourtes démontables sur plancher bois ;
- 2 cabanes démontables à ossature bois.
Le projet s’inscrit dans un secteur naturel à vocation d’hébergement touristique léger. Les constructions projetées sont conçues comme des ouvrages légers, démontables et réversibles, destinés à une occupation temporaire et saisonnière à usage de loisirs.
Le projet ne prévoit pas d’habitat permanent, ni d’emplacements nus pour tentes, caravanes ou camping-cars. Les seuls aménagements complémentaires concernent une zone de stationnement légère et perméable, les cheminements, un local technique / sanitaire démontable, les raccordements projetés et le dispositif d’assainissement compact. Aucune voirie lourde ni imperméabilisation significative n’est prévue.

1. Implantation générale
Les six habitations légères de loisirs sont implantées sur une emprise limitée d'environ 2 800 m² au sein de la parcelle ZI n°18, d’une superficie cadastrale totale de 139 451 m².
L’implantation retenue suit la topographie naturelle du terrain et limite les interventions sur le sol. Les constructions sont réparties afin de conserver une perception aérée du site et de préserver au maximum le caractère boisé et naturel du terrain.
Les cheminements prévus sont à vocation piétonne et d’entretien léger. Aucun stationnement nouveau n’est créé dans le cadre de la présente demande.

2. Principe de réversibilité
L’ensemble des habitations légères de loisirs est conçu suivant un principe de réversibilité.
Les constructions sont posées sur des planchers bois portés par des appuis ponctuels réversibles, de type pieux bois ou pieux vissés métalliques selon étude d’exécution. Aucun scellement béton et aucune fondation maçonnée ne sont prévus pour les HLL.
Ce principe constructif permet :
- de limiter l’impact sur le terrain naturel ;
- d’éviter les terrassements lourds ;
- de conserver la perméabilité du sol ;
- de permettre le démontage des ouvrages ;
- de restituer le terrain avec un impact limité en cas de dépose.
Le local technique / sanitaire commun reprend la même logique de réversibilité. Il est conçu comme une structure légère démontable, posée sur appuis réversibles, sans fondations maçonnées.

3. Tipis démontables
Les deux tipis sont constitués d’une structure légère démontable composée de perches bois formant un principe de tripode et d’une couverture textile tendue.
Caractéristiques générales :
- diamètre : environ 5,50 m ;
- hauteur maximale : environ 5,60 m ;
- structure : perches bois démontables ;
- couverture : toile textile tendue ;
- plancher : plancher bois posé sur appuis réversibles ;
- teinte générale : toile claire, beige ou écru, afin de limiter l’impact visuel dans le site naturel.
Les tipis sont assemblés sans fondation maçonnée. Le montage et le démontage sont réalisés manuellement ou avec un outillage léger, sans intervention lourde sur le terrain.

4. Yourtes démontables
Les deux yourtes sont conçues selon un principe traditionnel de structure légère circulaire.
Caractéristiques générales :
- diamètre : environ 5,50 m ;
- hauteur maximale : environ 3,90 m ;
- structure verticale : treillis bois ;
- charpente : perches bois rayonnantes vers une couronne centrale ;
- couverture : toile textile ;
- plancher : plancher bois posé sur appuis réversibles ;
- teinte générale : toile claire, beige ou écru, avec structure bois apparente ou naturelle.
Les yourtes sont assemblées à sec, sans fondation maçonnée et sans scellement béton. Leur principe constructif permet un démontage complet et une réversibilité de l’implantation.

5. Cabanes démontables à ossature bois
Les deux cabanes sont conçues comme des structures légères démontables en panneaux à ossature bois, préfabriquées en atelier puis assemblées sur site.
Caractéristiques générales :
- dimensions du volume principal : environ 5,00 m x 4,00 m ;
- surface déclarée : 20,00 m² par cabane, hors débords légers de toiture ;
- hauteur maximale au faîtage : environ 3,80 m ;
- pente de toiture : environ 15 % ;
- structure : ossature bois démontable ;
- assemblage : panneaux préfabriqués assemblés par boulonnage ;
- plancher : plancher bois sur appuis réversibles ;
- façades : bardage bois ventilé ;
- couverture : couverture légère, de type bac acier isolé ou équivalent ;
- teinte générale : bois naturel, teinte bois grisé ou teinte neutre s’intégrant au paysage.
Les cabanes sont posées hors sol, sans fondations maçonnées. Les assemblages mécaniques permettent le démontage des éléments sans démolition lourde.

6. Local technique / sanitaire démontable
Un local technique / sanitaire démontable est prévu afin de centraliser les usages communs nécessaires au fonctionnement saisonnier des HLL.
Ce local a vocation à regrouper :
- quatre éviers ;
- deux toilettes sèches ;
- deux bacs de collecte des déchets, dont un bac ordures ménagères et un bac de tri ;
- des casiers de rangement ;
- des points de recharge et prises de service selon étude électrique ;
- une zone technique liée aux usages communs.
Les HLL ne sont pas raccordées individuellement aux réseaux. Les usages liés à l’eau, à l’électricité, aux sanitaires, à la recharge et à la gestion des eaux grises sont centralisés au niveau de ce local.
Le local est conçu comme une structure légère, démontable et réversible :
- bardage bois naturel ;
- couverture légère de type bac acier teinte gris anthracite ;
- menuiseries bois ;
- pose sur appuis réversibles ;
- absence de fondation maçonnée.
Sa position a été déterminée afin de limiter les longueurs de réseaux, de rester accessible depuis les HLL et de permettre une exploitation simple et lisible du site.

7. Matériaux et aspect extérieur
Le projet privilégie des matériaux sobres, naturels et compatibles avec le contexte boisé du site.
Les matériaux principaux sont :
- bois naturel pour les planchers, structures, perches, bardages et menuiseries ;
- toile textile claire pour les tipis et yourtes ;
- couverture légère et discrète pour les cabanes et le local technique / sanitaire ;
- éléments d’assemblage mécaniques démontables.
Les teintes retenues seront sobres et non réfléchissantes :
- bois naturel ou bois grisé ;
- toile beige, écru ou ton naturel ;
- couverture de cabane et du local technique dans une teinte neutre et mate, de type gris anthracite.
L’objectif est de limiter l’impact visuel des constructions et d’assurer une insertion paysagère douce dans l’environnement existant.

8. Modalités d’exécution des travaux
Les travaux seront réalisés avec des moyens légers, adaptés à la sensibilité du site.
Les principales étapes d’exécution sont les suivantes :
- repérage précis des implantations sur site ;
- protection des arbres conservés et des zones non concernées par les travaux ;
- réalisation des appuis ponctuels réversibles ;
- pose des planchers bois ;
- montage des structures démontables ;
- pose des toiles, bardages et couvertures ;
- implantation du local technique / sanitaire démontable ;
- mise en place des raccordements projetés vers le local commun ;
- mise en place du dispositif d’assainissement autonome compact, après validation du SPANC ;
- nettoyage du site et remise en état des abords immédiats.
Aucun terrassement lourd n’est prévu pour les HLL. Les adaptations au terrain naturel seront limitées au strict nécessaire pour garantir la stabilité et la bonne implantation des planchers.
Les travaux liés au raccordement en eau potable, au raccordement électrique et au dispositif d’assainissement autonome seront réalisés selon les prescriptions des gestionnaires compétents et après validation des organismes concernés.

9. Gestion du terrain naturel
Le projet conserve le profil général du terrain naturel. Les plateformes bois permettent de s’adapter à la pente sans créer de remblais ou déblais importants.
Les eaux pluviales continueront à s’infiltrer naturellement dans le terrain. Les surfaces créées restent limitées et les constructions ne génèrent pas d’imperméabilisation lourde du sol.
La zone de stationnement est traitée de manière légère et perméable, sans création de voirie lourde ni revêtement imperméable significatif.

10. Arbres et intégration paysagère
Le terrain présente un caractère boisé marqué. Les arbres existants non concernés par les implantations sont conservés.
Le projet nécessite l’abattage et le dessouchage de 14 arbres situés dans l’emprise directe des implantations, des cheminements, du local technique / sanitaire et des aménagements strictement nécessaires au fonctionnement du projet.
Les suppressions sont limitées au strict besoin du projet. Les arbres conservés participent à l’intégration paysagère des habitations légères de loisirs et permettent de limiter leur visibilité depuis les abords du site.
Des plantations de remplacement pourront être prévues afin de maintenir le caractère végétal du terrain.

11. Accès, stationnement et cheminements
L’accès au site s’effectue depuis le chemin existant.
Le projet prévoit une zone de stationnement légère et perméable, localisée en partie basse du terrain, à proximité de l’accès existant. Cette zone permet l’accueil des véhicules des usagers, sans création de voirie lourde ni imperméabilisation significative.
Le stationnement prévu est limité à des places voitures. Aucun emplacement nu pour tente, caravane ou camping-car n’est créé.
Un cheminement piéton permet de relier la zone de stationnement, le local technique / sanitaire et les HLL. Les cheminements sont conçus de manière légère et réversible, sans création de voie lourde ni imperméabilisation importante.

Maitre d'ouvrage: NICOLAS RABOT 455 Chemin de Lasprades VAUDREUILLE FR	Ouvrage: Implantation de 6 HLL démontables Zone Ntc	Adresse du projet: 455 Chemin de Lasprades 31250 VAUDREUILLE
Références: section ZI parcelle 18 Date :06/07/2026	Planche: Notice Page 1/2	Echelle : N° de plan: DPC11

12. Gestion des déchets
La gestion des déchets est centralisée au niveau du local technique / sanitaire ou à proximité immédiate de l'accès, selon les modalités de collecte retenues par le service compétent.
Le projet prévoit deux bacs de collecte :
- un bac pour les ordures ménagères ;
- un bac pour le tri sélectif.
La SIPOM a été informée du projet. Le dispositif de collecte sera adapté en coordination avec le service compétent, après avis de la Communauté de Communes et validation du projet. Le principe retenu s'oriente vers une collecte au porte-à-porte ou un dispositif équivalent adapté à l'exploitation touristique du site.
Les bacs seront présentés à la collecte selon l'organisation définie avec le service compétent.


13. Alimentation en eau potable
Le projet prévoit un raccordement au réseau public d'eau potable.
Le compteur ou point de raccordement projeté est localisé sur le plan de masse. La distribution sera limitée au local technique / sanitaire commun, afin d'alimenter les points d'eau nécessaires au fonctionnement du site.
Les HLL ne sont pas raccordées individuellement au réseau d'eau potable.
Le tracé représenté sur les plans est un tracé de principe. Il sera précisé lors des démarches de raccordement auprès du gestionnaire compétent et selon les prescriptions techniques applicables.

14. Raccordement électrique
Le projet prévoit un raccordement électrique général destiné aux usages communs du local technique / sanitaire.
Le compteur électrique projeté est localisé sur le plan de masse. Les usages électriques seront limités aux besoins communs : éclairage ponctuel, recharge d'équipements, prises de service et besoins liés au fonctionnement du local technique / sanitaire.
Les HLL ne sont pas raccordées individuellement au réseau électrique. Les hébergements pourront fonctionner avec des luminaires sur batterie, éclairages portatifs ou dispositifs rechargeables.
Le tracé représenté sur les plans est un tracé de principe. Il sera précisé selon les prescriptions du gestionnaire du réseau électrique et selon étude technique ultérieure.

15. Eaux usées et assainissement
Les HLL ne comprennent pas de sanitaires individuels raccordés. Les usages sanitaires et les points d'eau sont regroupés au niveau du local technique / sanitaire.
Les toilettes prévues sont des toilettes sèches, ne générant pas d'eaux vannes à traiter par le dispositif d'assainissement.
Les eaux grises issues des évier et points d'eau communs seront traitées par un dispositif d'assainissement autonome compact de type filtre coco ou équivalent, dimensionné à titre indicatif sur une base minimale de 5 EH.
L'implantation et le dimensionnement définitifs du dispositif seront soumis à validation du SPANC. L'emprise représentée au plan est indicative et pourra être adaptée en fonction de l'étude de filière, de la nature du sol, des contraintes de pente, des distances réglementaires et des prescriptions du service compétent.

16. Réseaux et équipements
Les réseaux projetés sont limités au fonctionnement du local technique / sanitaire commun.
Le projet prévoit :
- un raccordement eau potable projeté ;
- un raccordement électrique projeté ;
- un dispositif d'assainissement autonome compact projeté ;
- un point de collecte des déchets ;
- des cheminements légers ;
- une zone de stationnement perméable.
Les raccordements et dispositifs techniques seront réalisés selon les prescriptions des gestionnaires compétents et des services concernés.

17. Conclusion
Le projet propose une implantation limitée de six habitations légères de loisirs démontables, dans une logique de faible impact, de réversibilité et d'intégration paysagère.
Les matériaux choisis, les modes de pose hors sol, l'absence de fondations maçonnées pour les HLL, le maintien du caractère naturel du terrain, le traitement perméable du stationnement et la centralisation des équipements dans un local technique / sanitaire démontable permettent de préserver l'identité paysagère du site.
Les constructions projetées sont légères, démontables, réversibles et adaptées à une occupation temporaire et saisonnière à usage de loisirs.
La surface totale créée par les six habitations légères de loisirs est de 135,04 m², correspondant à deux tipis démontables de 23,76 m² chacun, deux yourtes démontables de 23,76 m² chacune et deux cabanes démontables de 20,00 m² chacune.
Le local technique / sanitaire, le stationnement léger, le raccordement en eau potable, le raccordement électrique, la gestion des déchets et le dispositif d'assainissement compact constituent des aménagements complémentaires nécessaires au fonctionnement du projet, tout en conservant une logique de sobriété, de réversibilité et de limitation de l'impact sur le site.

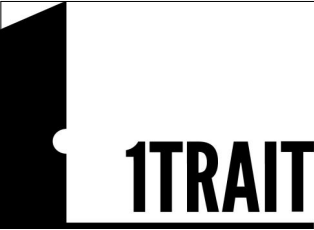	Maître d'ouvrage: NICOLAS RABOT #Client E-mail +33 6 31 32 48 94 Parcelle: N° Z118		Ouvrage : 455 Chemin de Lasprades 31250 VAUDREUILLE		Projet REL
	Maître d'oeuvre : 1 TRAIT STUDIO ANASTASSIYA et EHOUARN ISSAIKINA-GOURDRÉ 06.95.09.40.76 info@1trait.com		Planche: Notice Page 2/2	Echelle :	N° de projet : (088)
				N° de plan: DPC11	Date : 06/07/2026